



Общество с ограниченной ответственностью
«АСУ Инжиниринг»

АСУ ИНЖИНИРИНГ

ПАО «Казаньоргсинтез»

МОДЕРНИЗАЦИЯ (МИГРАЦИЯ) АСУ ТП НИТКИ КОМПАУНДИРОВАНИЯ Д

ТЕХНОРАБОЧИЙ ПРОЕКТ

Схема подключения сетей обмена информацией

КОС25001-157- АСУ.С10

Главный инженер проекта

10.02.2025

Ф.Н. Баянов


Инв. № подл.	Подпись и дата	Взам. инв. №

Согласовано			
Инв. N° подл.	Подпись и дата	Взам. инв. N°	

Перечень элементов

Поз.	Обознач.	Наименование	Кол.	Примечание
1	Шкаф №2	Шкаф сетевой коммутационный	1	Сущ.
2	ТКШ03	Шкаф сетевой коммутационный	1	Сущ.
3	ТКШ04	Шкаф сетевой коммутационный	1	Сущ.
4	Шкаф №10	FCS0315	1	Сущ.
5	ШС	Шкаф серверный	1	Сущ.
6	KVM-T	KVM передатчик	1	Зам.
7	KVM-R1, KVM-R2	KVM приемник	2	KVM-R1-зам. KVM-R2-нов.
8	SW, SW08, SW09	Сетевой коммутатор Hirschmann MACH104-20TX-F	3	Сущ.


						КОС25001-157-АСУ.С10			
						ПАО «Казаньоргсинтез»			
Изм.	Кол.уч.	Лист	№ док.	Подпись	Дата	Модернизация (миграция) АСУ ТП нитки компаундирования Д	Стадия	Лист	Листов
Разраб.	Худяков			<i>Худяков</i>	05.2025		Р	1	6
Пров.	Иванов			<i>Иванов</i>	05.2025				
						Схема подключения сетей обмена информацией			
Н. контр.	Зырянова			<i>Зырянова</i>	05.2025				
ГИП	Баянов			<i>Баянов</i>	05.2025				

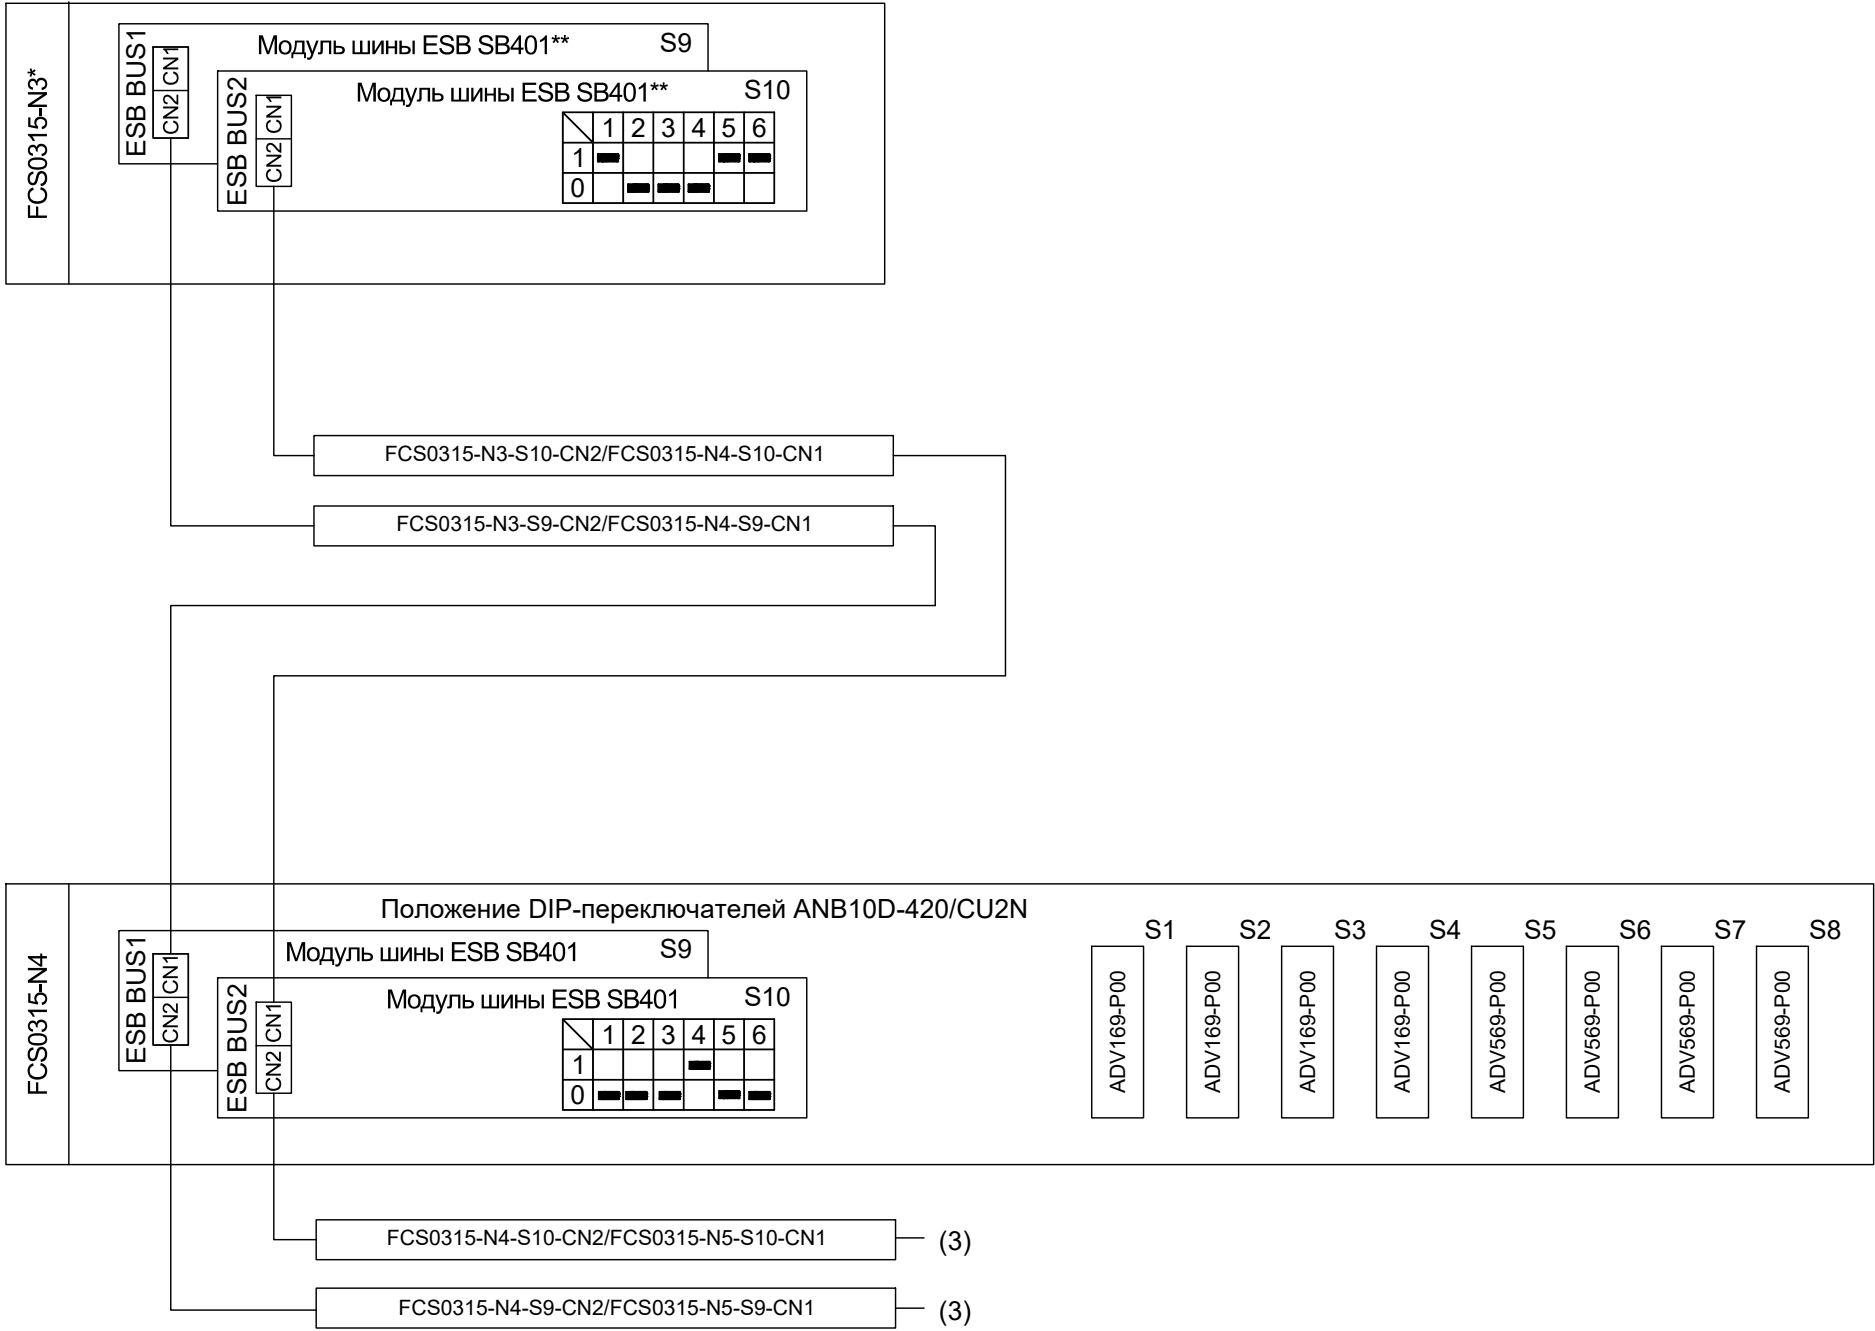


* - Существующее оборудование
** - Существующие модули EC401 с корзины N3 установить на корзину N9. Новые модули SB401 в составе корзины N9 установить на корзину N3, учитывая положение DIP переключателей.

Инв. N° подл.	Подпись и дата	Взам. инв. N°


Шкаф №10 FCS0315

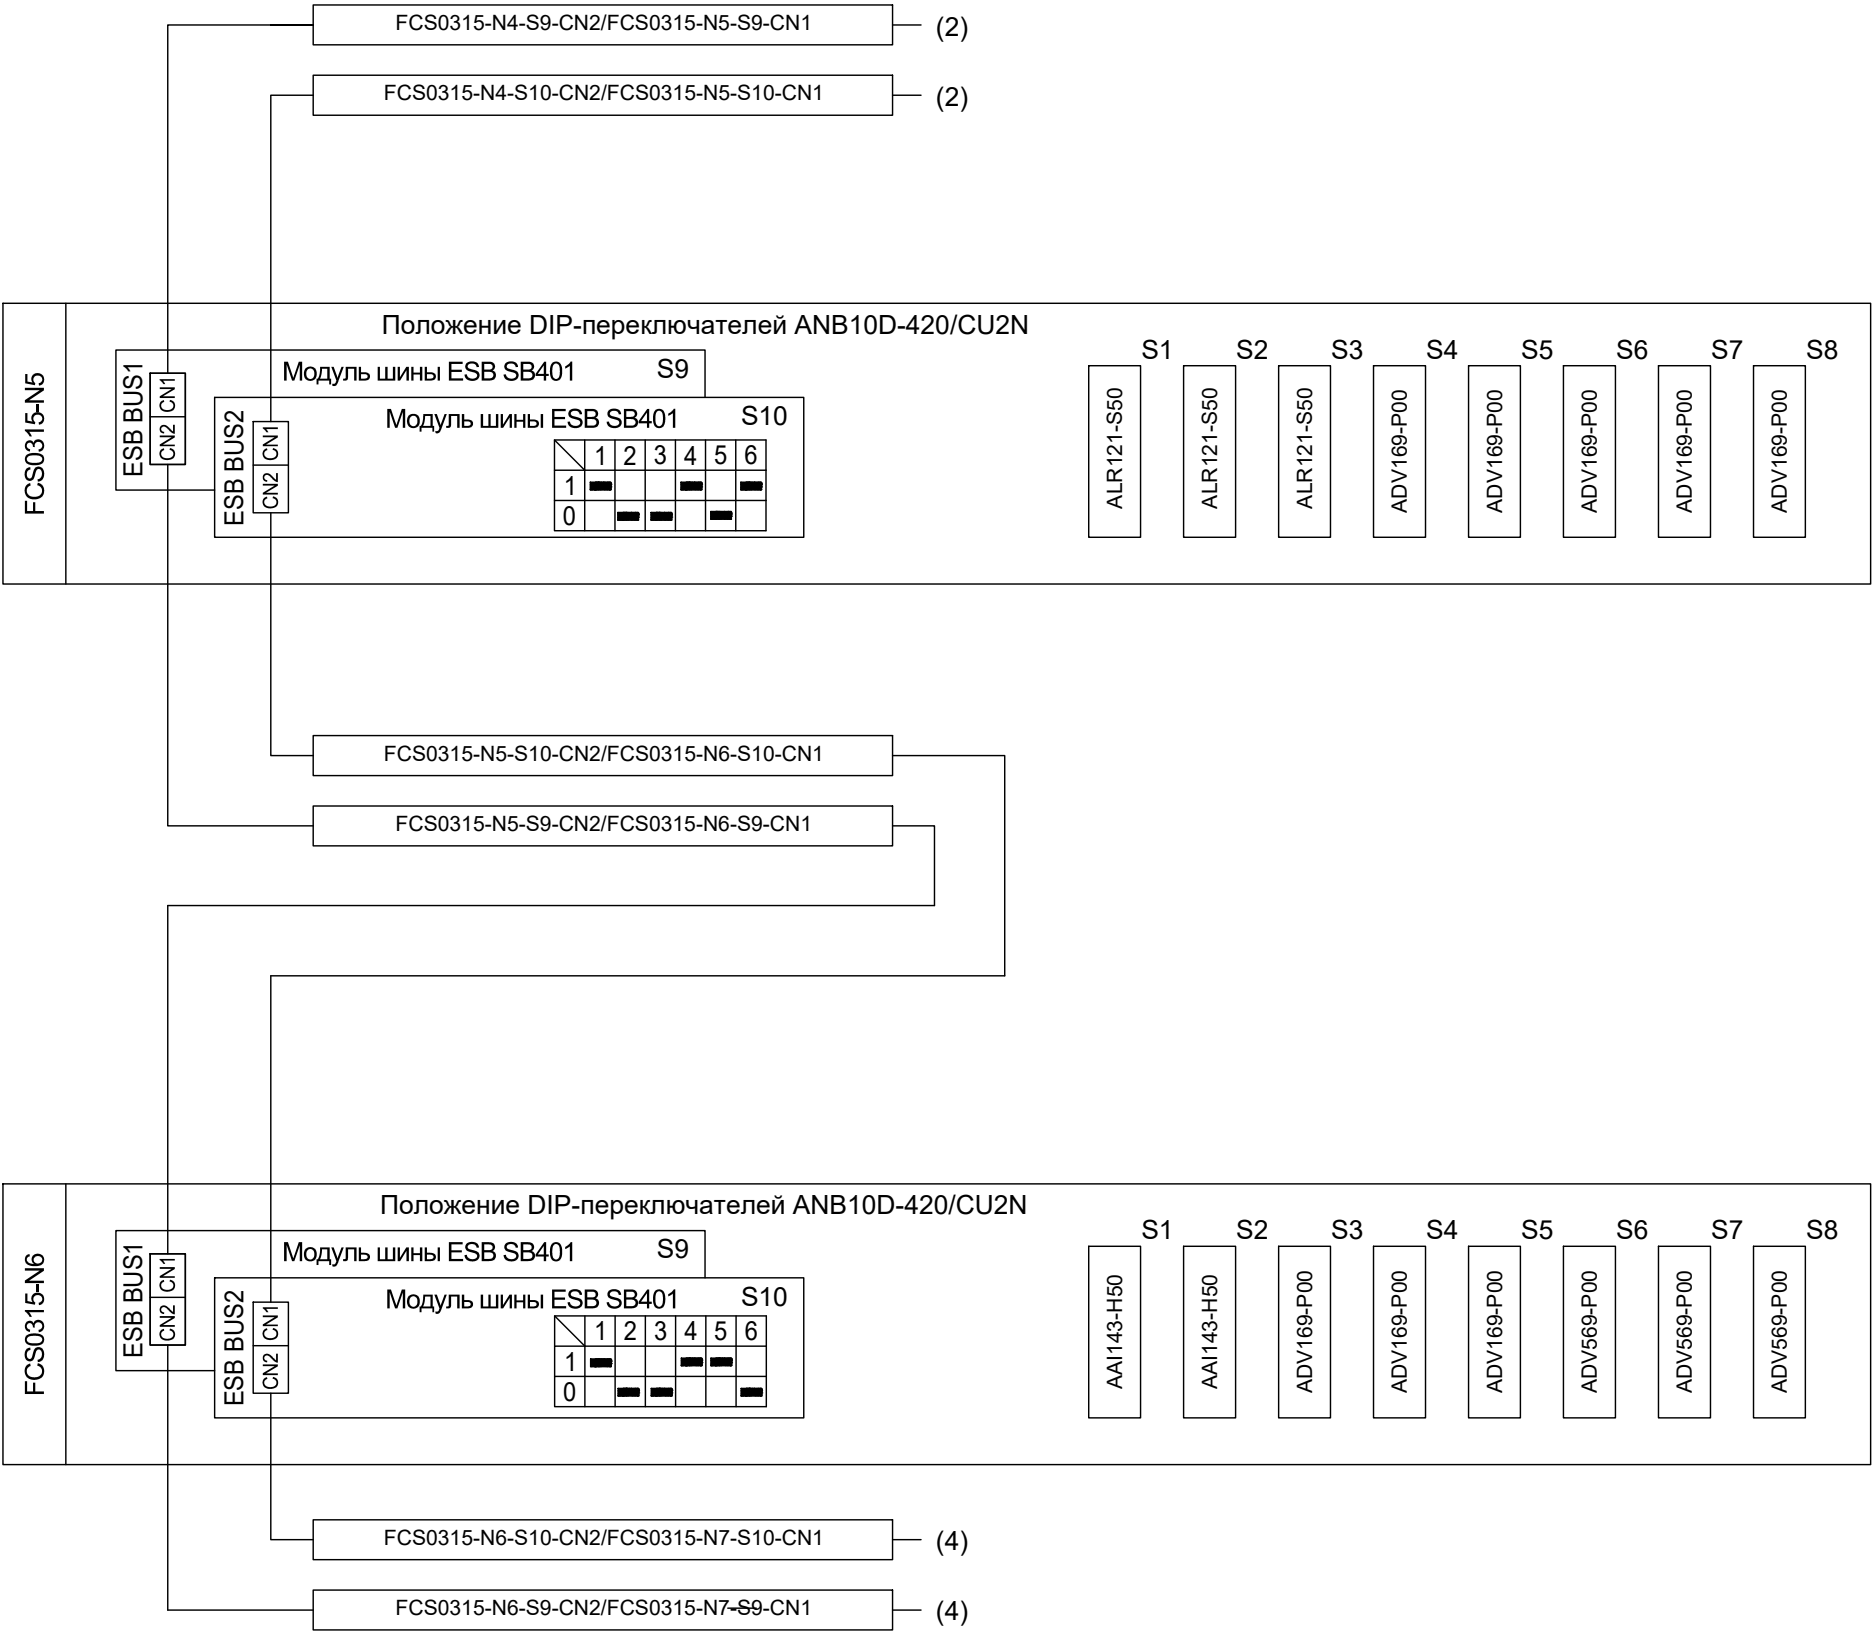

Шкаф №10 FCS0315

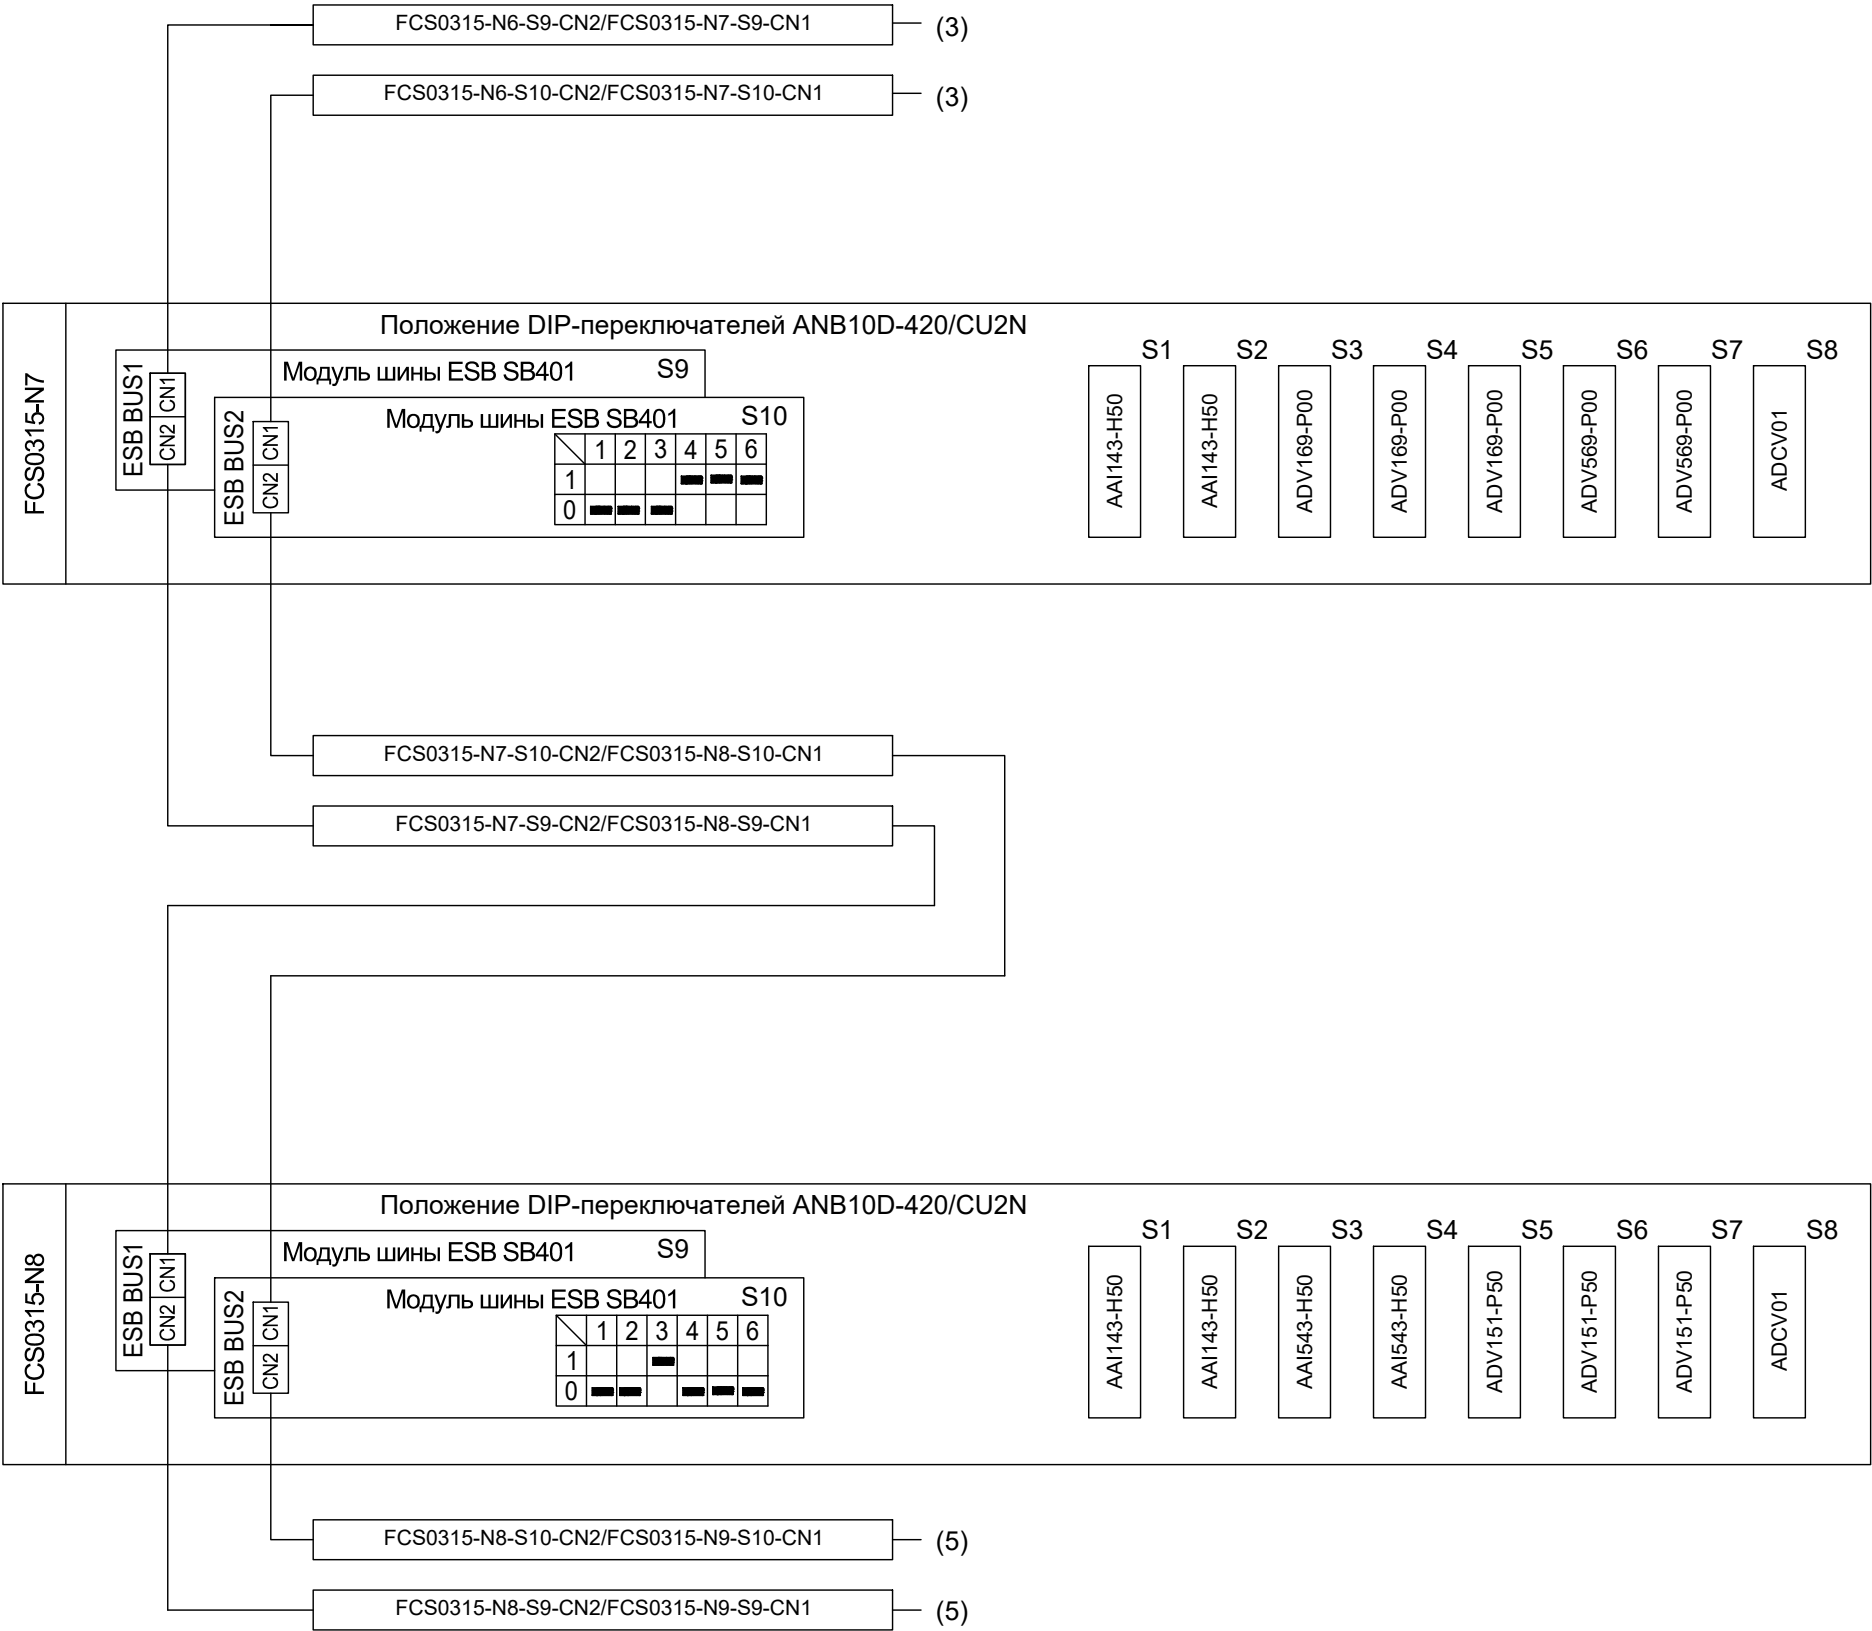

Шкаф №10 FCS0315

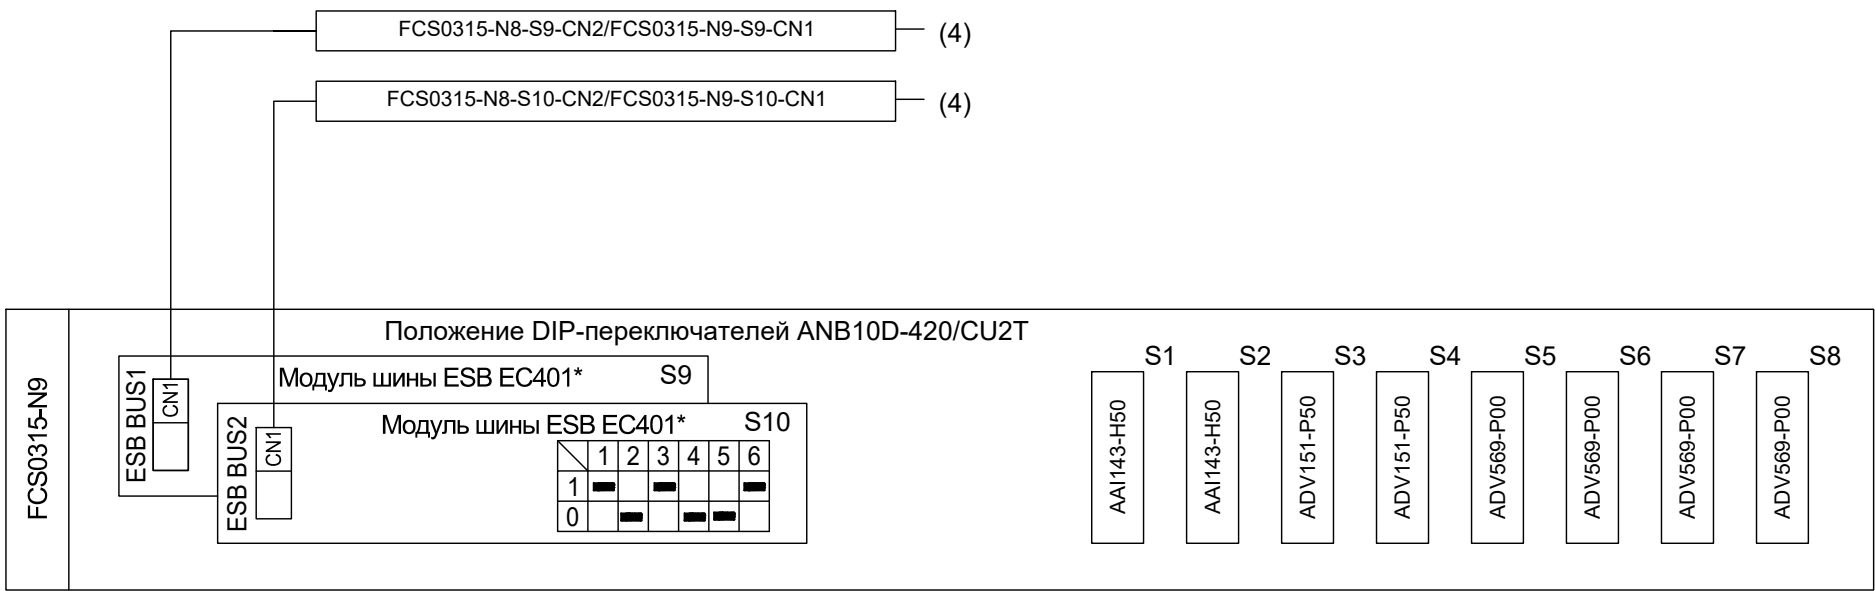

* - Новые модули SB401 в составе корзины N9 установить на корзину N3. Существующие модули EC401 с корзины N3 установить на корзину N9, учитывая положение DIP переключателей.

Инов. N° подл.	Подпись и дата	Взам. инв. N°

						КOC25001-157-ACУ.C10	Лист
Изм.	Кол.уч.	Лист	№ док	Подпись	Дата		5