



Общество с ограниченной ответственностью
«АСУ Инжиниринг»

АСУ ИНЖИНИРИНГ

ПАО «Казаньоргсинтез»

МОДЕРНИЗАЦИЯ (МИГРАЦИЯ) АСУ ТП НИТКИ КОМПАУНДИРОВАНИЯ Д

ТЕХНОРАБОЧИЙ ПРОЕКТ

Схема заземления

КОС25001-157- АСУ.С12

Главный инженер проекта

15.04.2025


Ф.Н. Баянов

Инв. № подл.	Подпись и дата	Взам. инв. №

Перечень элементов

Поз.	Обознач.	Наименование	Кол.	Примечание
1	Шкаф №16	Реле DI/DO	1	Нов.
2	Шкаф №17	Реле DI/DO	1	Нов.
3	Шкаф №18	Реле DI/DO	1	Нов.
4	Шкаф №19	ШРП	1	Нов.

Контур защитного заземления *

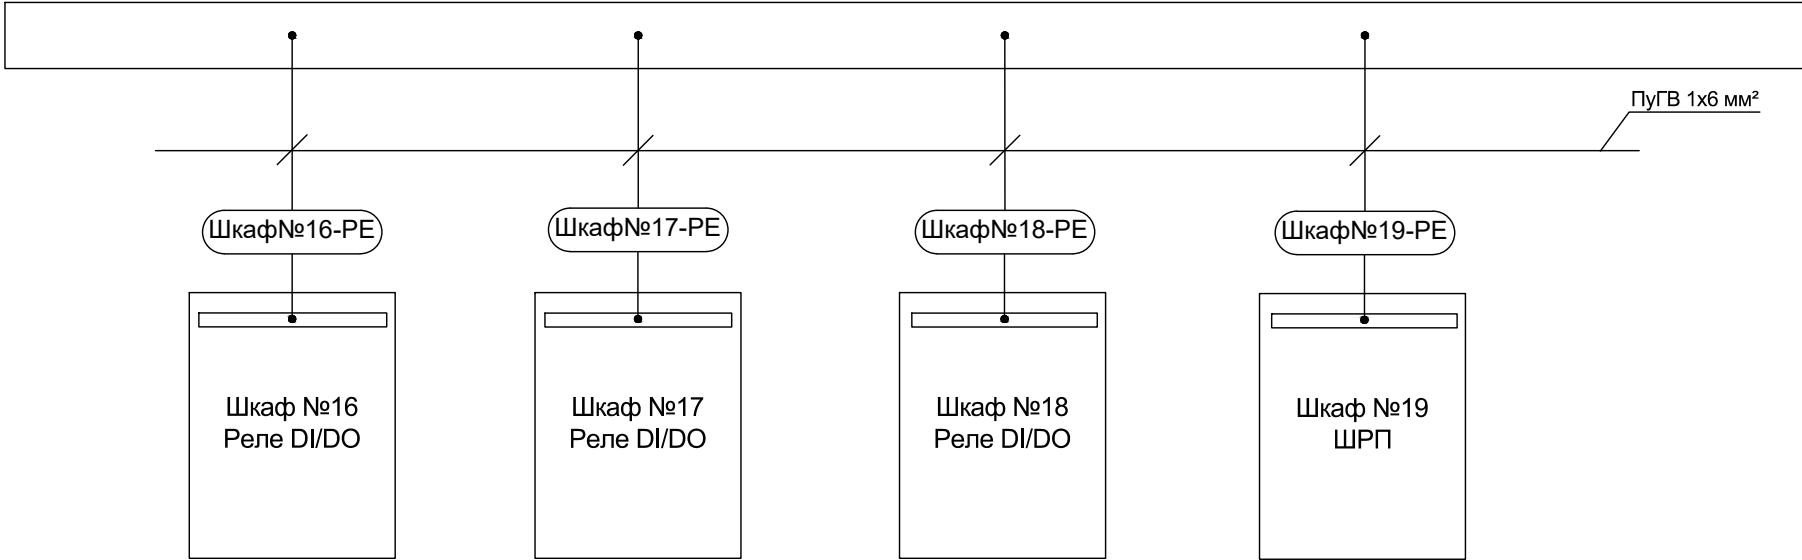

* - Точка подключения указана в разделе ЭМ

Согласовано			
Взам. инв. №			
Подпись и дата			
Инв. № подл.			

						КОС25001-157-АСУ.С12			
						ПАО «Казаньоргсинтез»			
Изм.	Кол.уч.	Лист	№ док.	Подпись	Дата	Модернизация (миграция) АСУ ТП нити компаундирования Д	Стадия	Лист	Листов
Разраб.	Худяков			<i>Худяков</i>	04.2025		Р		1
Пров.	Иванов			<i>Иванов</i>	04.2025				
						Схема заземления	 АСУ ИНЖИНИРИНГ		
Н. контр.	Зырянова			<i>Зырянова</i>	04.2025				
ГИП	Баянов			<i>Баянов</i>	04.2025				