



Общество с ограниченной ответственностью
«АСУ Инжиниринг»

АСУ ИНЖИНИРИНГ

ПАО «Казаньоргсинтез»

МОДЕРНИЗАЦИЯ (МИГРАЦИЯ) АСУ ТП НИТКИ КОМПАУНДИРОВАНИЯ Д

ТЕХНОРАБОЧИЙ ПРОЕКТ

План расположения

КОС25001-157- АСУ.С8

Главный инженер проекта

10.02.2025

Ф.Н. Баянов

Инв. № подл.	Подпись и дата	Взам. инв. №

Согласовано

Взам. инв. №


Подпись и дата

Инв. № подл.

Перечень элементов - (начало)				
Поз.	Обознач.	Наименование	Кол.	Примечание
Операторная к.157				
1	COPERION 1	Шкаф управления COPERION	1	Сущ.
2	COPERION 2	Шкаф управления COPERION	1	Сущ.
3	COPERION 3	Шкаф управления COPERION	1	Сущ.
4	COPERION 4	Шкаф управления COPERION	1	Сущ.
5	COPERION 5	Шкаф управления COPERION	1	Сущ.
6	COPERION 6	Шкаф управления COPERION	1	Сущ.
7	COPERION 7	Шкаф управления COPERION	1	Сущ.
8	COPERION 8	Шкаф управления COPERION	1	Сущ.
9	COPERION 9	Шкаф управления COPERION	1	Сущ.
10	KRAUSS 1	Шкаф управления KRAUSS	1	Сущ.
11	KRAUSS 2	Шкаф управления KRAUSS	1	Сущ.
12	Шкаф пневмотранспорта	Пневмотранспорт порошка "А" и "Б"	1	Сущ.
13	ЩК	Щит питания кондиционеров	1	Сущ.
14	ШУ	Шкаф +B26 Бункер готов. продук.	1	Сущ.
15	Шкаф ШРП	Шкаф ШРП К-157	1	Сущ.
16	Шкаф №19	ШРП	1	Новый
17	Шкаф серверный	Шкаф серверный	1	Сущ.
18	-	FCS0316	1	Сущ.
19	ТКСШ03	Шкаф сетевой комутационный	1	Сущ.
20	Шкаф №10	FCS0315 Блок интеграции контроллеров экструдеров	1	Сущ., меняется
21	Шкаф №09	FCS0314 Система транспорта порошка к экструдерам "А","В","С"	1	Сущ.
22	Шкаф №01	Система транспорта порошка ПЭ "Coperion C". Реле DO, DI. Датчики Namur и реле	1	Сущ.
23	Шкаф №12	FCS0317, AI	1	Сущ., меняется
24	Шкаф №13	Реле DI/DO, AI	1	Сущ., меняется
25	Шкаф №14	AI, AO, Namur	1	Сущ., меняется
26	Шкаф №16	Реле DI/DO	1	Новый
27	Шкаф №17	Реле DI/DO	1	Новый
28	Шкаф №18	Реле DI/DO	1	Новый
28	MOTAN	Шкаф птранс-т.гран MOTAN	1	Сущ., демонтируется

Перечень элементов - (конец)				
Поз.	Обознач.	Наименование	Кол.	Примечание
30	-	Шкаф УДС	1	Сущ.
31	Шкаф №15	ШРП	1	Сущ.
32	ШРП АСУТП	Шкаф ШРП АСУТП +A992В	1	Сущ.
33	+A962С	Шкаф +A962С	1	Сущ.
34	-	Щит КИПиА	1	Сущ.
35	-	АРМ оператора KRAUSS	1	Сущ.
36	-	АРМ оператора COPERION	1	Сущ.
37	-	АРМ оператора LineC	1	Сущ.
38	-	АРМ оператора LineA	1	Сущ.
39	HIS0364	АРМ инженера	1	Сущ.
40	HIS0353	АРМ оператора	1	Сущ.
41	HIS0354	АРМ оператора	1	Сущ.
42	К1	Короб напольный металлический 100х200 (ВхШ)	1	Новый
43	К2	Короб вертикальный металлический	1	Сущ.
44	К3	Короб вертикальный металлический	1	Новый
Операторная к.159				
1	ТКСШ04	Шкаф сетевой коммутационный	1	Сущ.
2	ШУ159-1	Шкаф управления экструзионной линией D	1	Сущ., меняется
3	LP-159/2	Шкаф управления COPERION	1	Сущ.
4	PLC-159/1	Шкаф управления COPERION	1	Сущ., меняется
5	ШУ159-2	Шкаф управления экструзионной линией D	1	Сущ., меняется
6	ШУ159-3	Шкаф управления экструзионной линией D	1	Сущ.,меняется
7	ШБ159-1	Шкаф барьеров искробезопасности Namur	1	Сущ.
8	HIS0349	АРМ оператора	1	Новый
КОС25001-157-АСУ.С8				
ПАО «Казаньоргсинтез»				
Изм.	Кол.уч.	Лист	№ док.	Подпись
Разраб.	Корчагин		04.2025	
Пров.	Иванов		04.2025	
Модернизация (миграция) АСУ ТП нитки компаундирования Д		Стадия	Лист	Листов
		Р	1	3
План расположения				
Н. контр.	Зырянова		04.2025	
ГИП	Баянов		04.2025	

Операторная к.157
План на отм. +7,200

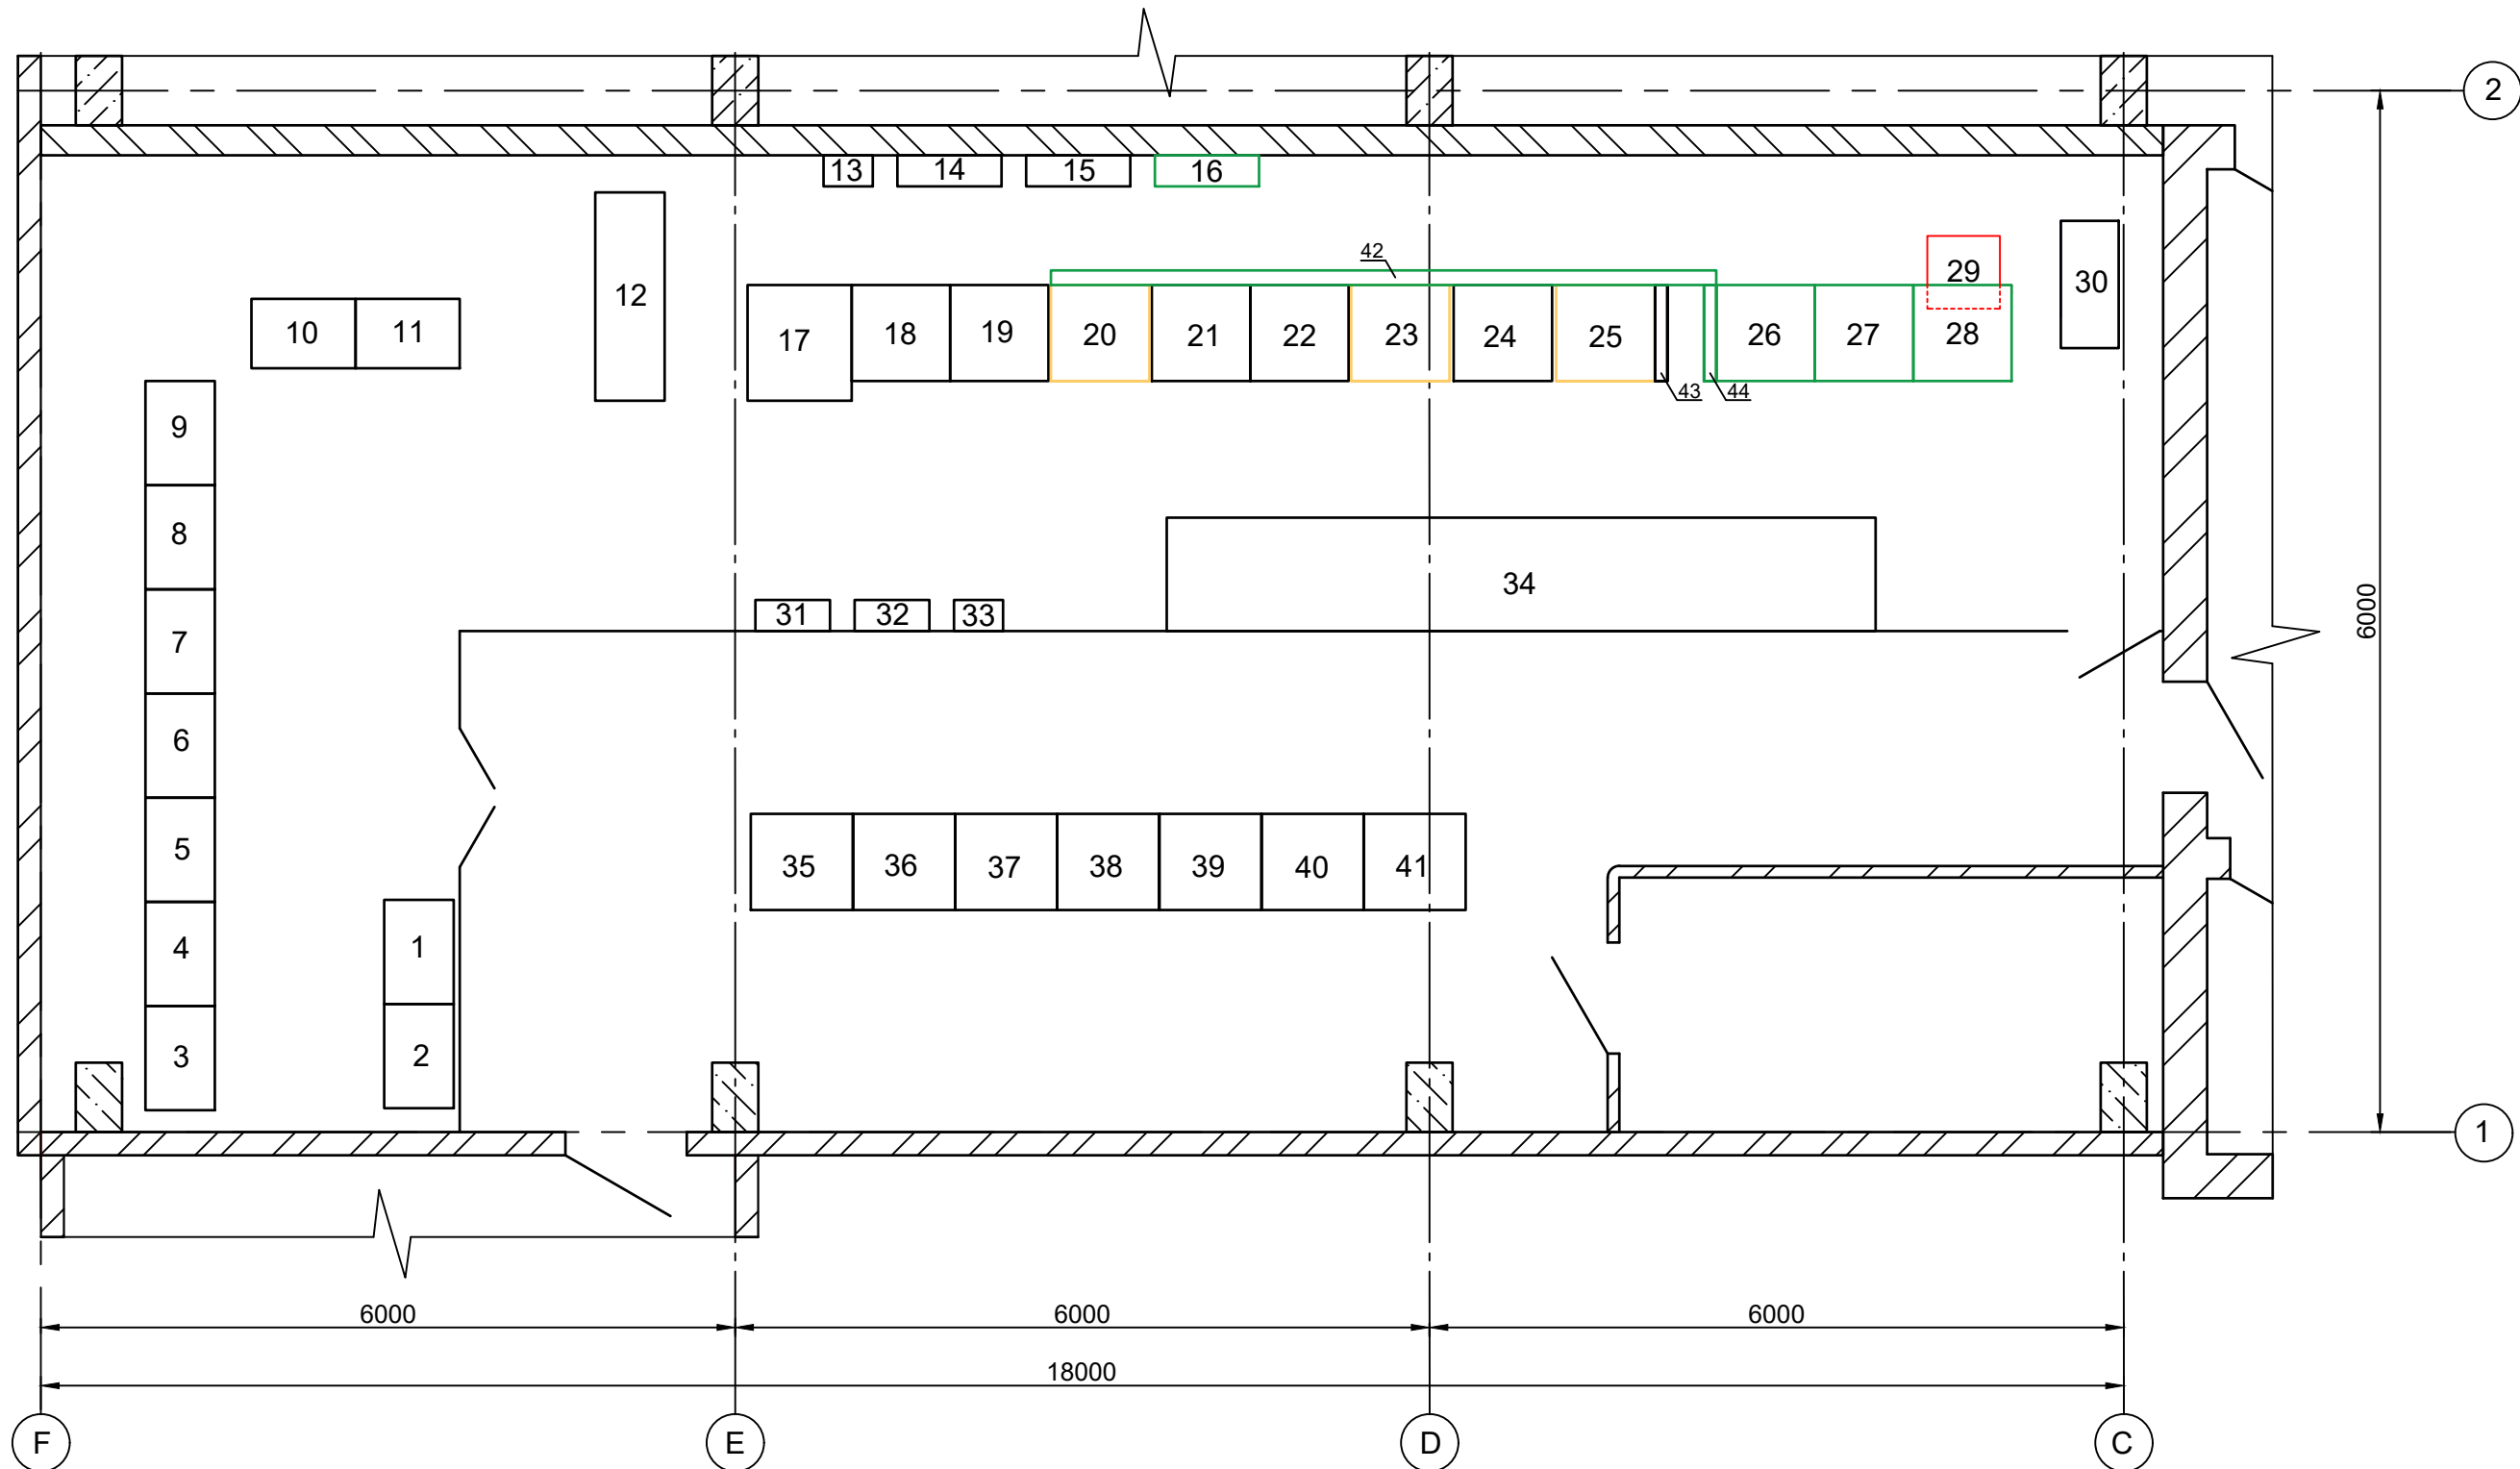


Условные обозначения:
черный - существующее оборудования без изменений;
оранжевый - существующее оборудования с изменениями;
зеленый - новое оборудование;
красный - демонтируемое существующее оборудование.

Демонтаж шкафа «MOTAN» (поз.29) не входит в объем работ по данному проекту.
Демонтаж осуществляется Заказчиком самостоятельно.

Инва. N° подл.	Подпись и дата	Взам. инв. N°

Изм.	Кол.уч.	Лист	№ док.	Подпись	Дата	KOC25001-157-ACU.C8	Лист 2

Операторная к.159
План на отм. +1,200

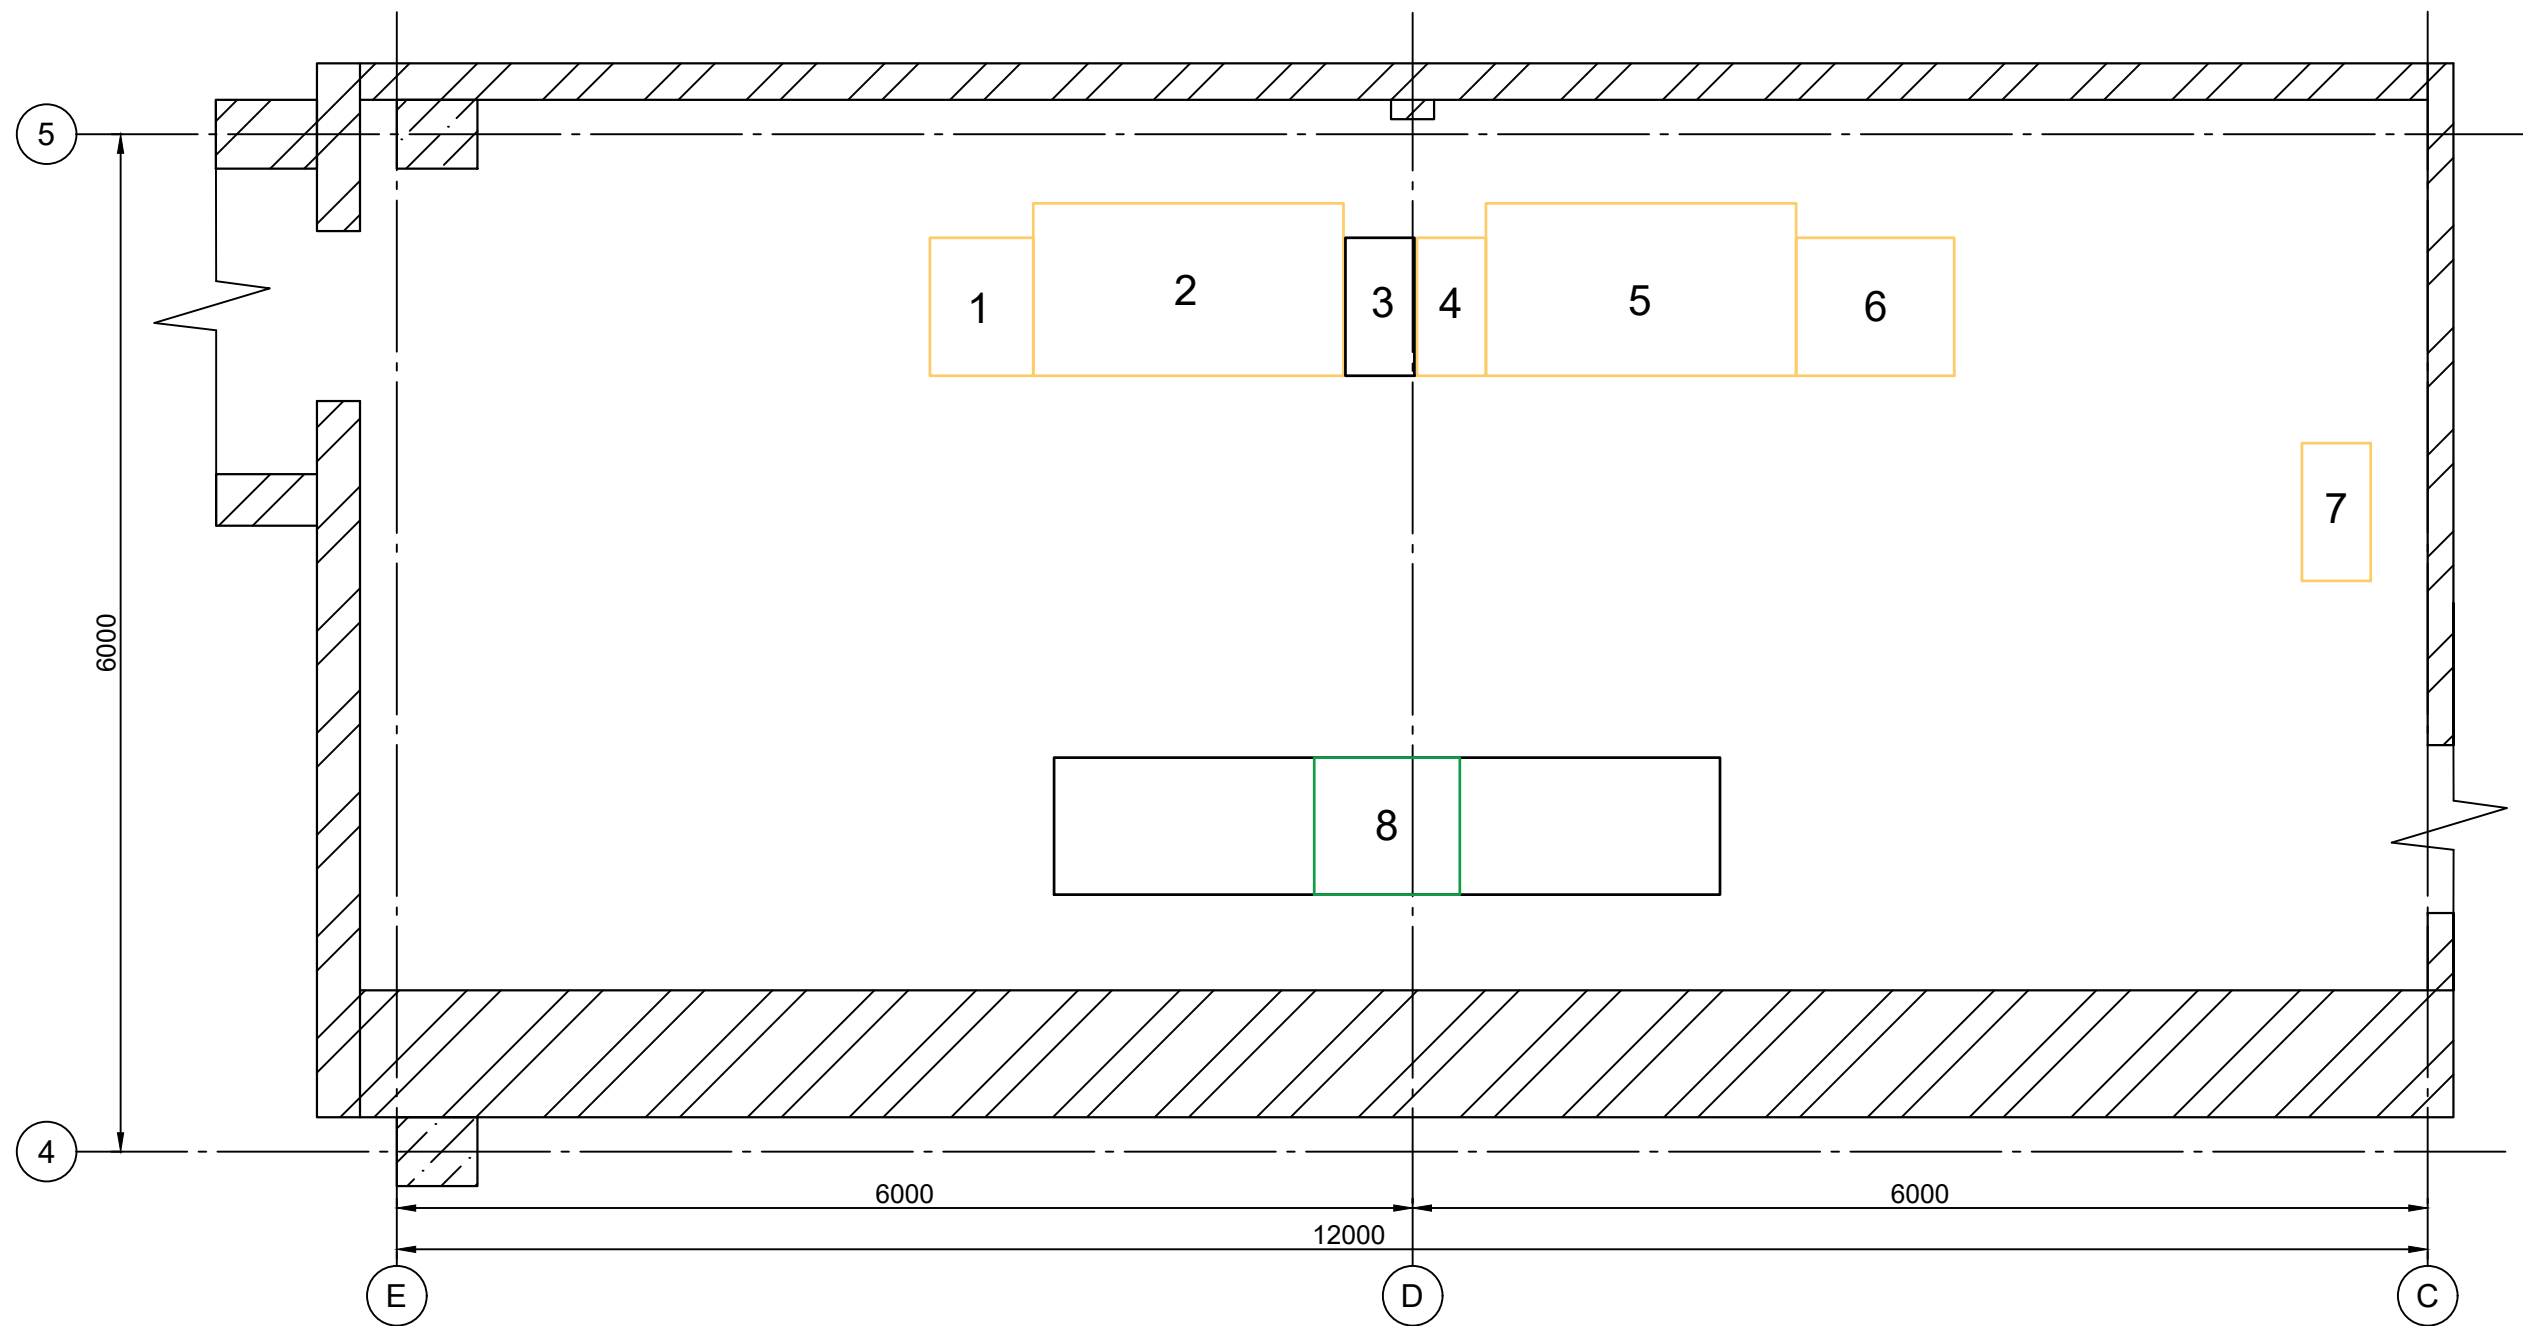

Условные обозначения:
черный - существующее оборудования без изменений;
оранжевый - существующее оборудования с изменениями;
зеленый - новое оборудование.

Инв. N° подл.	Подпись и дата	Взам. инв. N°

Изм.	Кол.уч.	Лист	№ док.	Подпись	Дата

KOC25001-157-ACU.C8