



Общество с ограниченной ответственностью

«АСУ Инжиниринг»

ПАО «Казаньоргсинтез»

МОДЕРНИЗАЦИЯ (МИГРАЦИЯ) АСУ ТП НИТКИ КОМПАУНДИРОВАНИЯ Д

Шкаф №14 AI, АО, Namur

Альбом 08

Всего альбомов 18


КОС25001-157-АСУ.08

Главный инженер проекта

28.01.2025

Ф.Н. Баянов

Инв. № подл.	Подп. и дата	Взам. инв. №	Инв. № дубл.	Подп. и дата

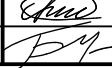Перв. примен.	№ строки	Формат	Обозначение	Наименование	Кол. листов	№ экз.	Примечание			
			1	KOC25001-157-АСУ.08.ОП	Шкаф №14 AI, АО, Namur. Описание альбома	2				
			2	KOC25001-157-АСУ.08.С	Шкаф №14 AI, АО, Namur. Спецификация	2				
			3	KOC25001-157-АСУ.08.МЧ	Шкаф №14 AI, АО, Namur. Монтажный чертёж	4				
			4	KOC25001-157-АСУ.08.Э4	Шкаф №14 AI, АО, Namur. Схема электрическая соединений	2				
			5	KOC25001-157-АСУ.08.ПЭ4	Шкаф №14 AI, АО, Namur. Перечень элементов	1				
			6	KOC25001-157-АСУ.08.ТБ	Шкаф №14 AI, АО, Namur. Таблица соединений	2				
Справ. №										
Подп. и дата										
Инв. № дубл.										
Взам. инв. №										
Подп. и дата										
Инв. № подл.										
KOC25001-157-АСУ.08.ОП										
Изм	Лист	№ докум	Подп.	Дата	Шкаф №14 AI, АО, Namur. Описание альбома		Лит.	Лист	Листов	
Разраб.	Аликин			01.2025			Т		2	2
Пров.	Гиниятулин			01.2025						
Н. контр.	Зырянова			01.2025						
Утв.	Баянов			01.2025						
							 АСУ ИНЖИНИРИНГ			

Перв. примен.		Поз.	Обозначение	Наименование и техническая характеристика	Описание	Код оборудования, изделия, материала	Завод-изготовитель	Количество	Ед. измерения	Масса единицы, кг.	Примечание
		1	2	3	4	5	6	7	8	9	10
		Защитные устройства									
		1	ХТЗ	Предохранитель 5x20 мм	Предохранитель 2 А, 250 В, 5x20 мм	2 А, 250 В		18	шт.		
Справ. №		Усилители, регуляторы									
		2	ISD4 ... ISD8	Терминальная плата	Терминальная плата DI-сигналов	HiCTB16-YC3-RRB-AK-CC-DX32	P+F	5	шт.		
		3	ISD4.1 ... ISD4.16, ISD5.1 ... ISD5.16, ISD6.1 ... ISD6.16, ISD7.1 ... ISD7.16, ISD8.1 ... ISD8.16	Барьер искрозащиты	Барьер искрозащиты DI-сигналов	HiC2842	P+F	80	шт.		
		Кабели									
		4		Провод ПуГВнг(А)-LS 1.5 мм² RD	ПУГВ 1.5 мм² RD (красный) ГОСТ 31947-2012	ПУГВ-1.5-RD		15	м		
		5		Провод ПуГВнг(А)-LS 1.5 мм² DKBU	ПУГВ 1.5 мм² DKBU (синий) ГОСТ 31947-2012	ПУГВ-1.5-DKBU		10	м		
		6		Держатель маркировки проводника STC	Держатель маркировки проводника STC-1-30 Сечение провода: 0.5 — 2.5 мм² Длина: 30 мм	765130	ELEGIR	30	шт.		
		7		Маркер для контейнеров	Маркер для установки в держатели маркеров HiC-R-30-4.6-W До 17 символов. Высота: 4.6 мм Длина: 30 мм	419304602	ELEGIR	30	шт.		
		8		Наконечник НШВИ 1.0–8	Наконечник штыревой втулочный изолированный, одинарный	79438	KBT	30	шт.		
		Принадлежности корпуса для внутренней установки									
Подп. и дата		9		Дин-рейка перфорированная OMEGA 3AF, 35x15 мм	Дин-рейка перфорированная OMEGA 3AF, 35x15 мм	02150	DKC	2	м		
		Кабельные каналы									
Инв. № дубл.		10		RL12 60x100	Короб перфорированный, серый RL12 60x100	00162RL	DKC	2	м		
Взам. инв. №											
Подп. и дата											
Инв. № подл.											

Изм	Лист	№ докум	Подп.	Дата
Разраб.	Аликин			01.2025
Пров.	Гиниятулин			01.2025
Н. контр.	Зырянова			01.2025
Утв.	Баянов			01.2025


КОС25001-157-АСУ.08.С		
Шкаф №14 AI, АО, Namur. Спецификация		
Лит.	Лист	Листов
Т	1	2
		

КОС25001-157-АСУ.08_Rev.0_04

Формат А3

Инв. № подл.	Подп. и дата	Взам. инв. №	Инв. № дубл.	Подп. и дата	Справ. №	Перв. примен.	ККС25001-157-АСУ.08.МЧ	
Вид спереди Вид сзади Вид сбоку	
<table><tr><td>Изм.</td><td>Лист</td><td>№ докум</td><td>Подп.</td><td>Дата</td><td rowspan="3">Шкаф №14 AI, АО, Namur. Монтажный чертёж</td><td>Лит.</td><td>Масса</td><td>Масштаб</td></tr><tr><td>Разраб.</td><td>Аликин</td><td></td><td><i>Аликин</i></td><td>01.2025</td><td>Т</td><td></td><td>1:10</td></tr><tr><td>Пров.</td><td>Гиниятулин</td><td></td><td><i>Гиниятулин</i></td><td>01.2025</td><td></td><td></td><td></td></tr><tr><td></td><td></td><td></td><td></td><td></td><td></td><td>Лист 1</td><td colspan="2">Листов 4</td></tr><tr><td>Н. контр.</td><td>Зырянова</td><td></td><td><i>Зырянова</i></td><td>01.2025</td><td></td><td colspan="3" rowspan="2"> АСУ ИНЖИНИРИНГ</td></tr><tr><td>Утв.</td><td>Баянов</td><td></td><td><i>Баянов</i></td><td>01.2025</td><td></td></tr></table>							Изм.	Лист	№ докум	Подп.	Дата	Шкаф №14 AI, АО, Namur. Монтажный чертёж	Лит.	Масса	Масштаб	Разраб.	Аликин		<i>Аликин</i>	01.2025	Т		1:10	Пров.	Гиниятулин		<i>Гиниятулин</i>	01.2025										Лист 1	Листов 4		Н. контр.	Зырянова		<i>Зырянова</i>	01.2025		 АСУ ИНЖИНИРИНГ			Утв.	Баянов		<i>Баянов</i>	01.2025	
Изм.	Лист	№ докум	Подп.	Дата	Шкаф №14 AI, АО, Namur. Монтажный чертёж	Лит.	Масса	Масштаб	
Разраб.	Аликин		<i>Аликин</i>	01.2025		Т		1:10	
Пров.	Гиниятулин		<i>Гиниятулин</i>	01.2025	
						Лист 1	Листов 4	
Н. контр.	Зырянова		<i>Зырянова</i>	01.2025		 АСУ ИНЖИНИРИНГ	
Утв.	Баянов		<i>Баянов</i>	01.2025	
ККС25001-157-АСУ.08_Rev.0_04	
Формат А3	


Вид сзади без дверей

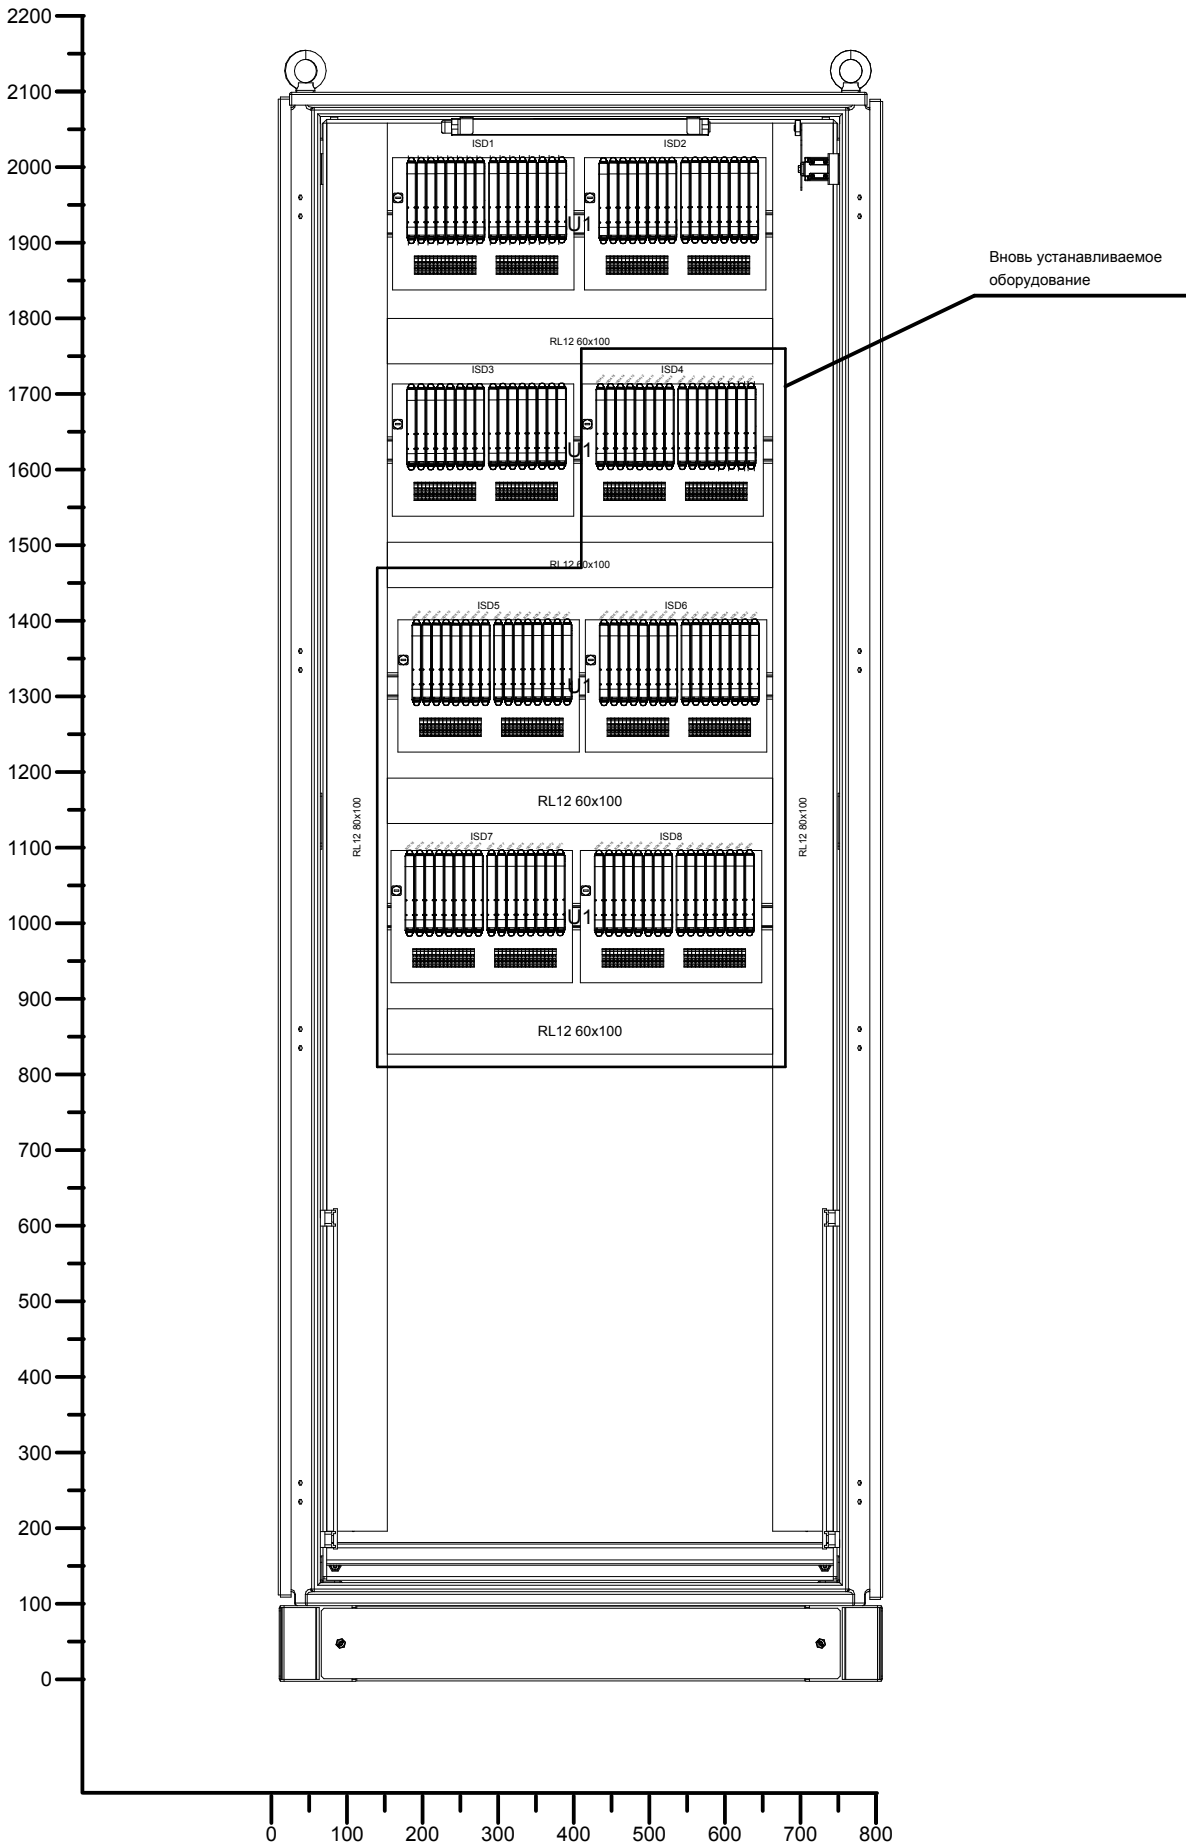


Инв. № подл.	Подп. и дата	Взам. инв. №	Инв. № дубл.	Подп. и дата

					КОС25001-157-АСУ.08.МЧ	Лист
Изм	Лист	№ докум	Подп.	Дата		2


Вид слева

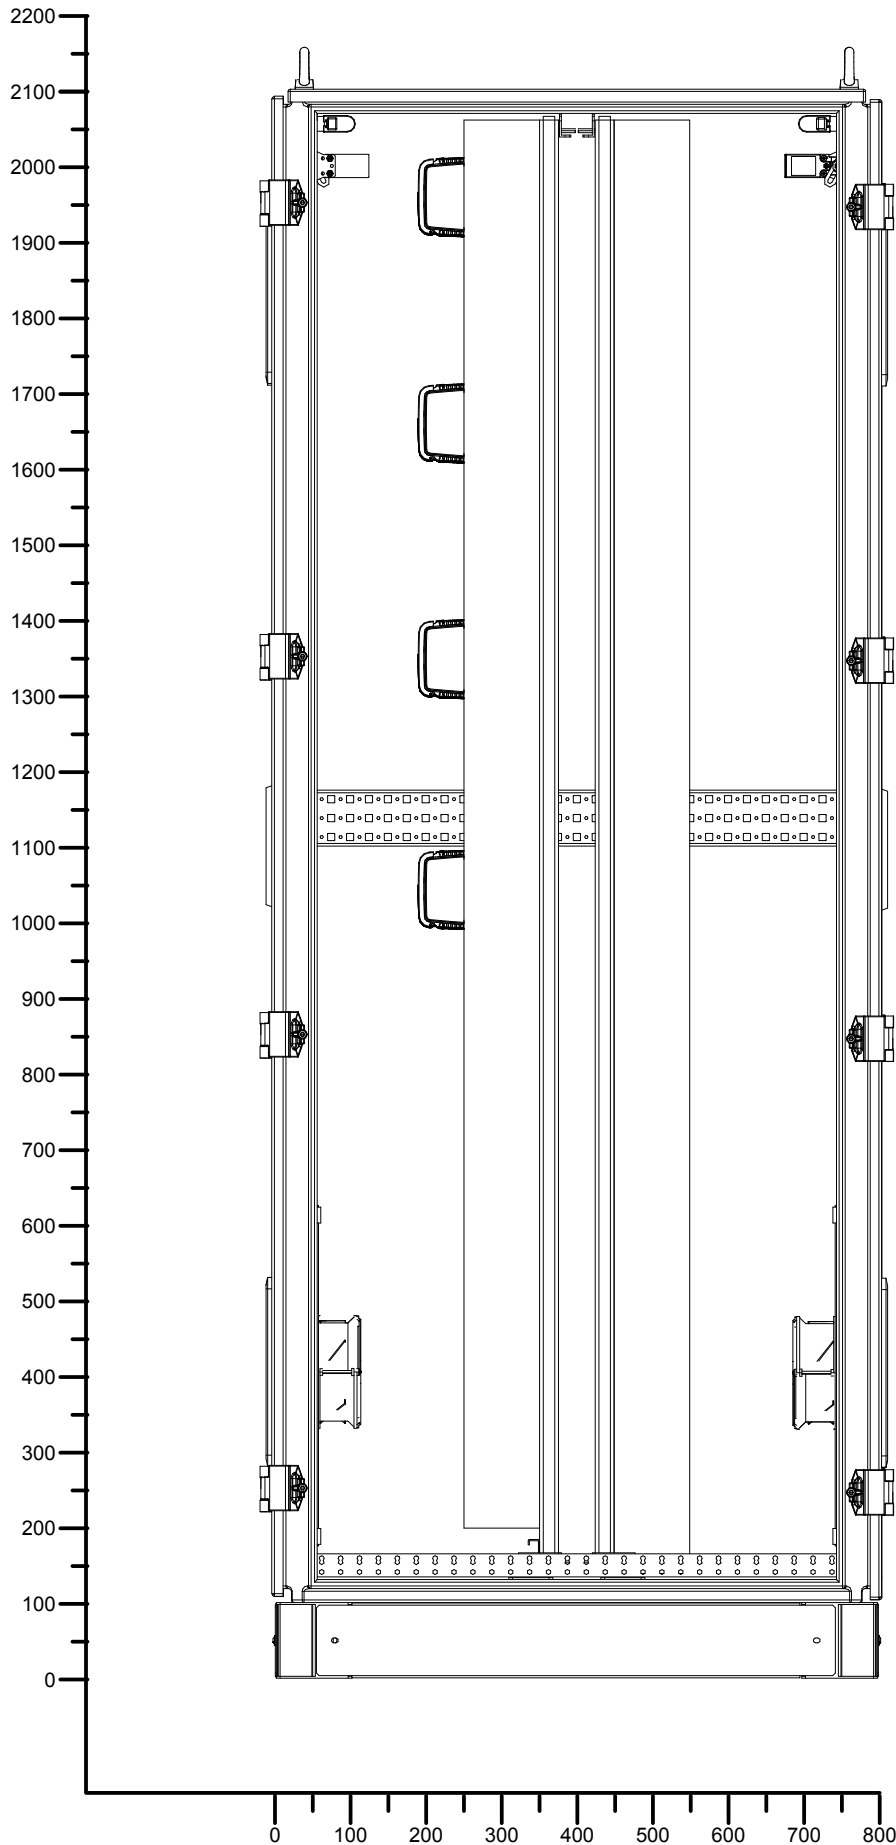


Вид справа

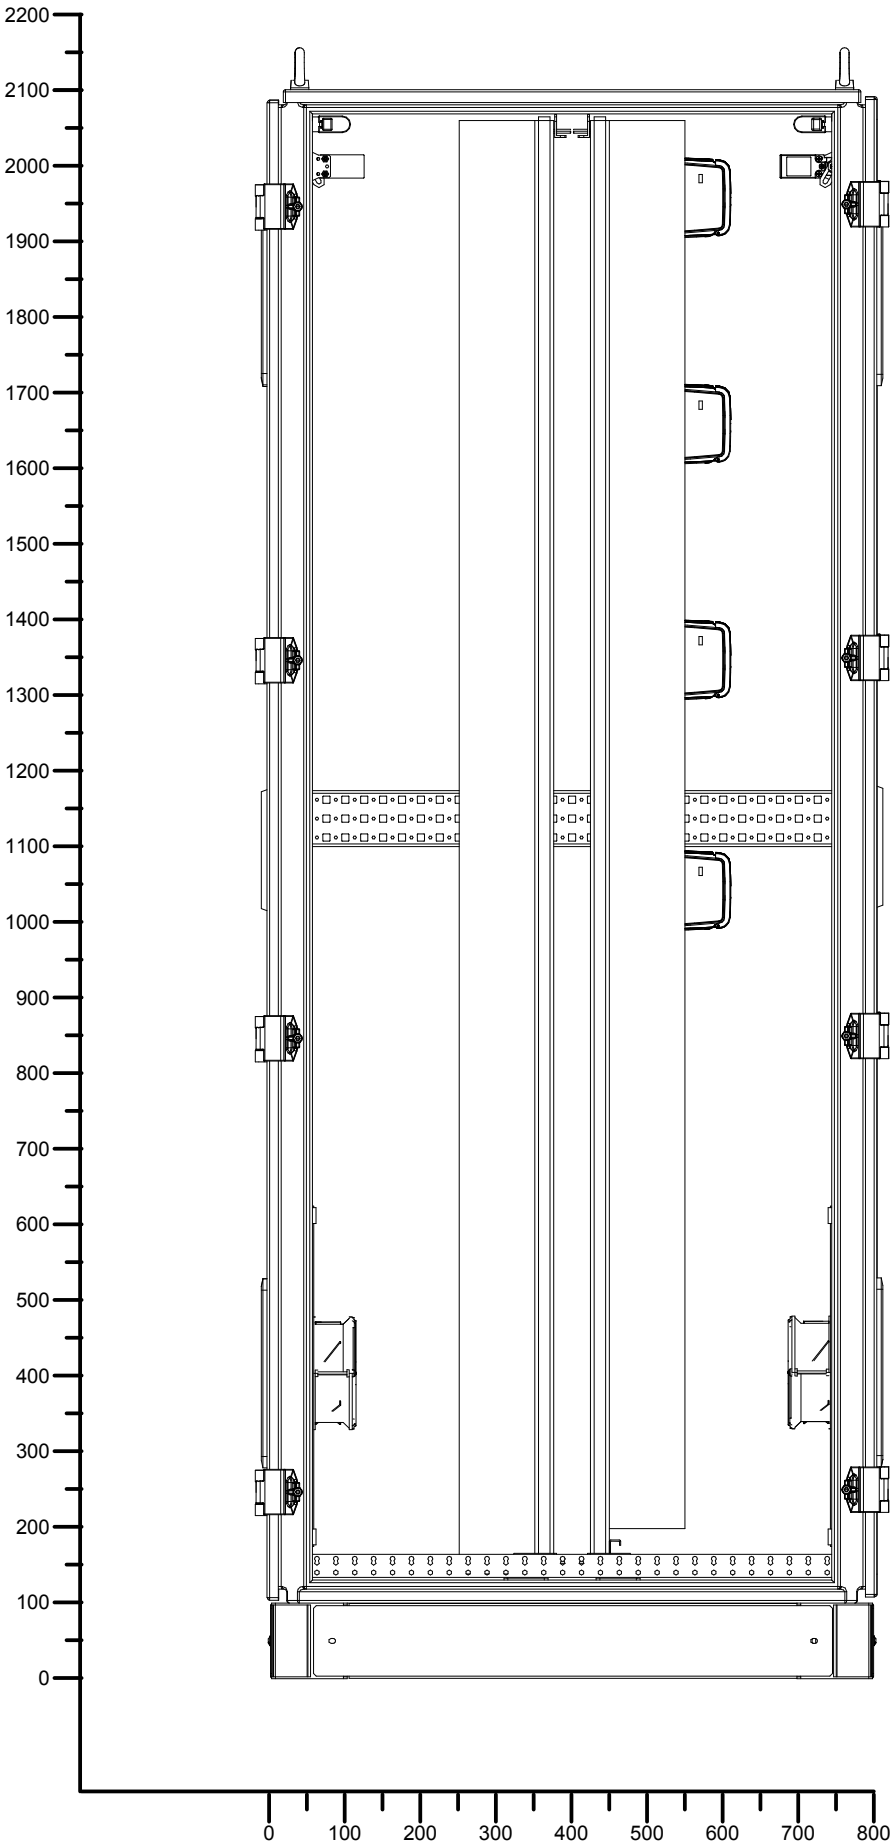

Вид сверху

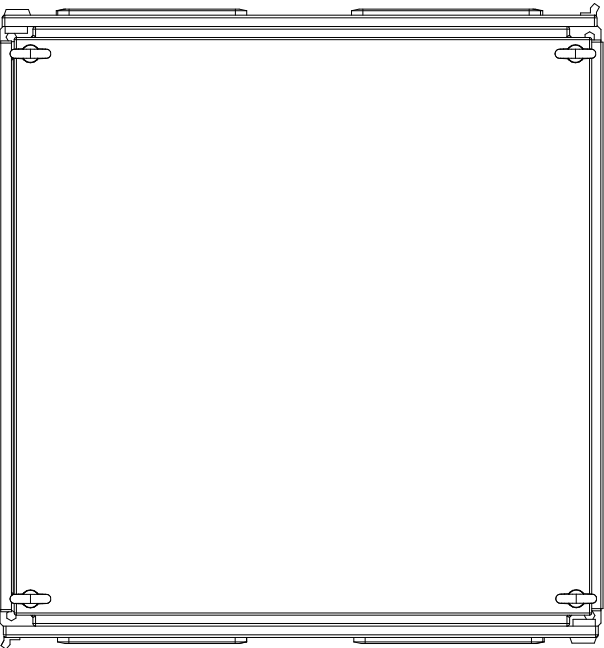


Вид снизу

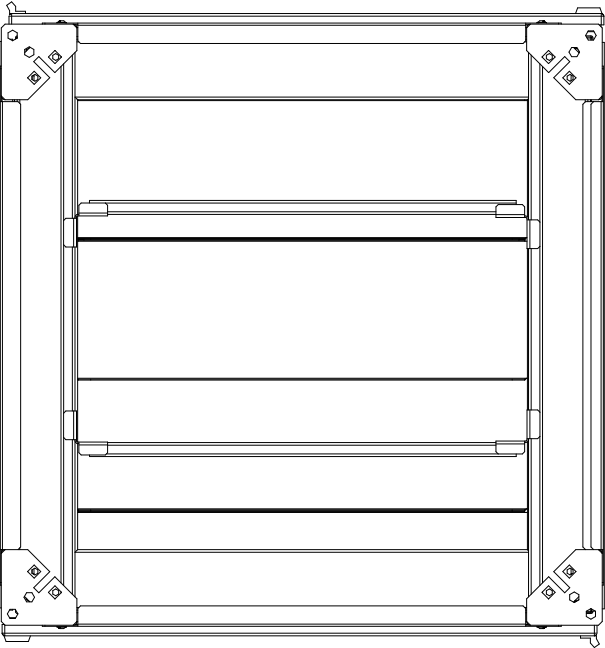

Инд. № подл.	Подп. и дата	Взам. инв. №	Инд. № дубл.	Подп. и дата


Изм	Лист	№ докум	Подп.	Дата

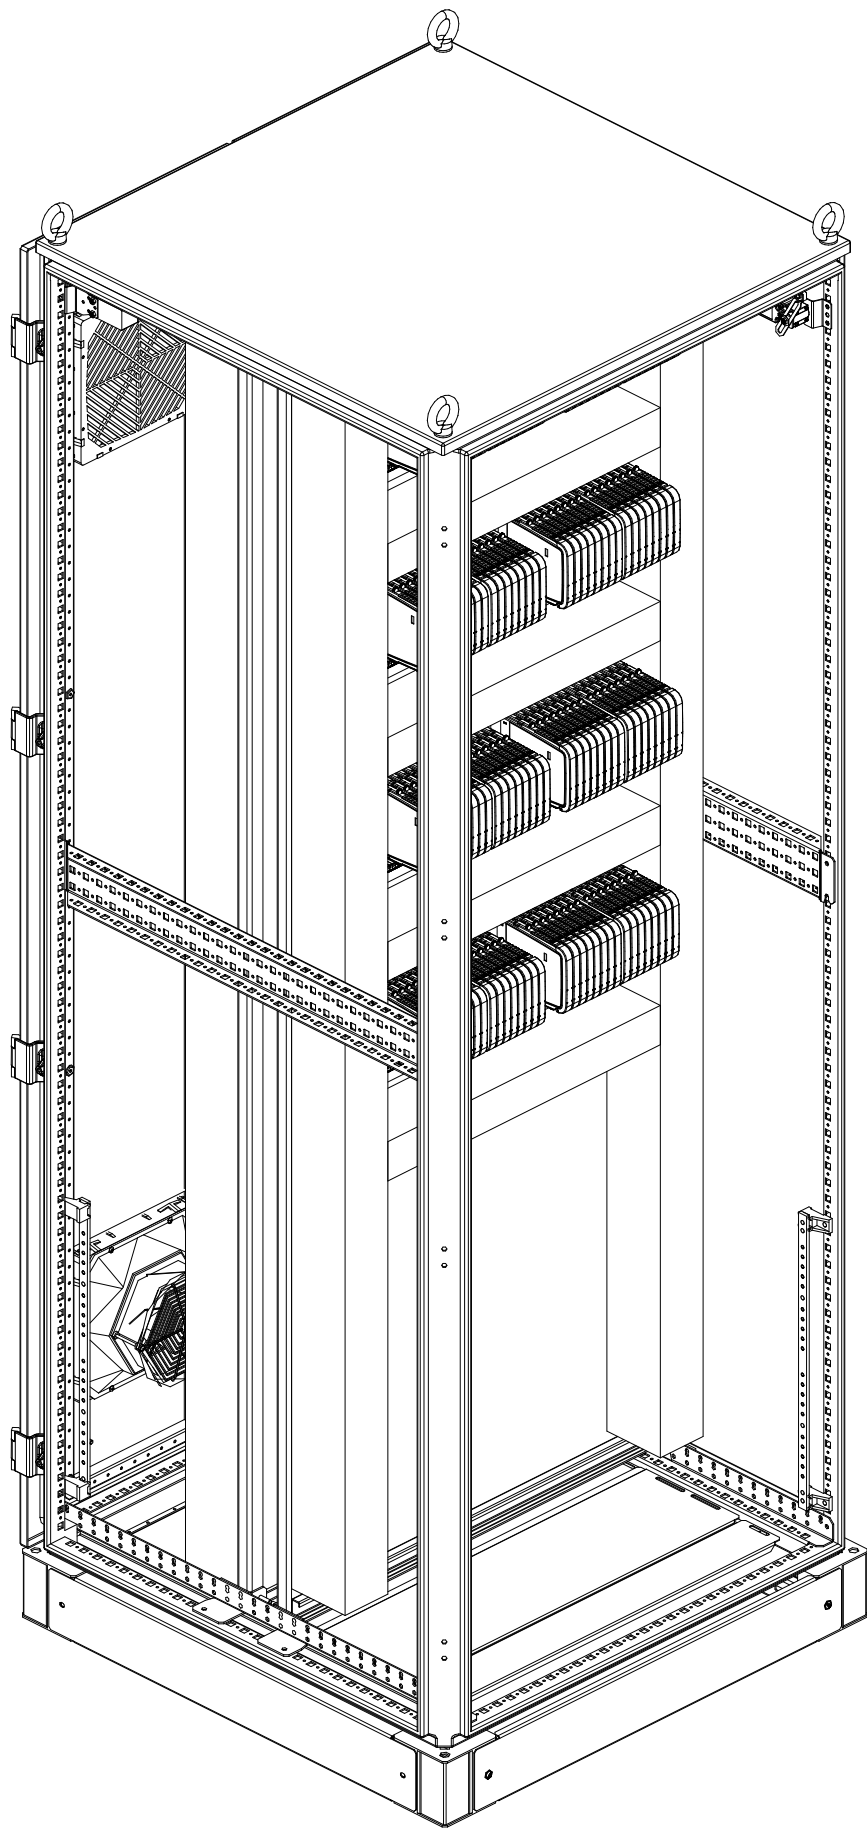


Инв. № подл.	Подп. и дата	Взам. инв. №	Инв. № дубл.	Подп. и дата

Изм	Лист	№ докум	Подп.	Дата

Схема электропитания 24 VDC (клеммники питания существующие)

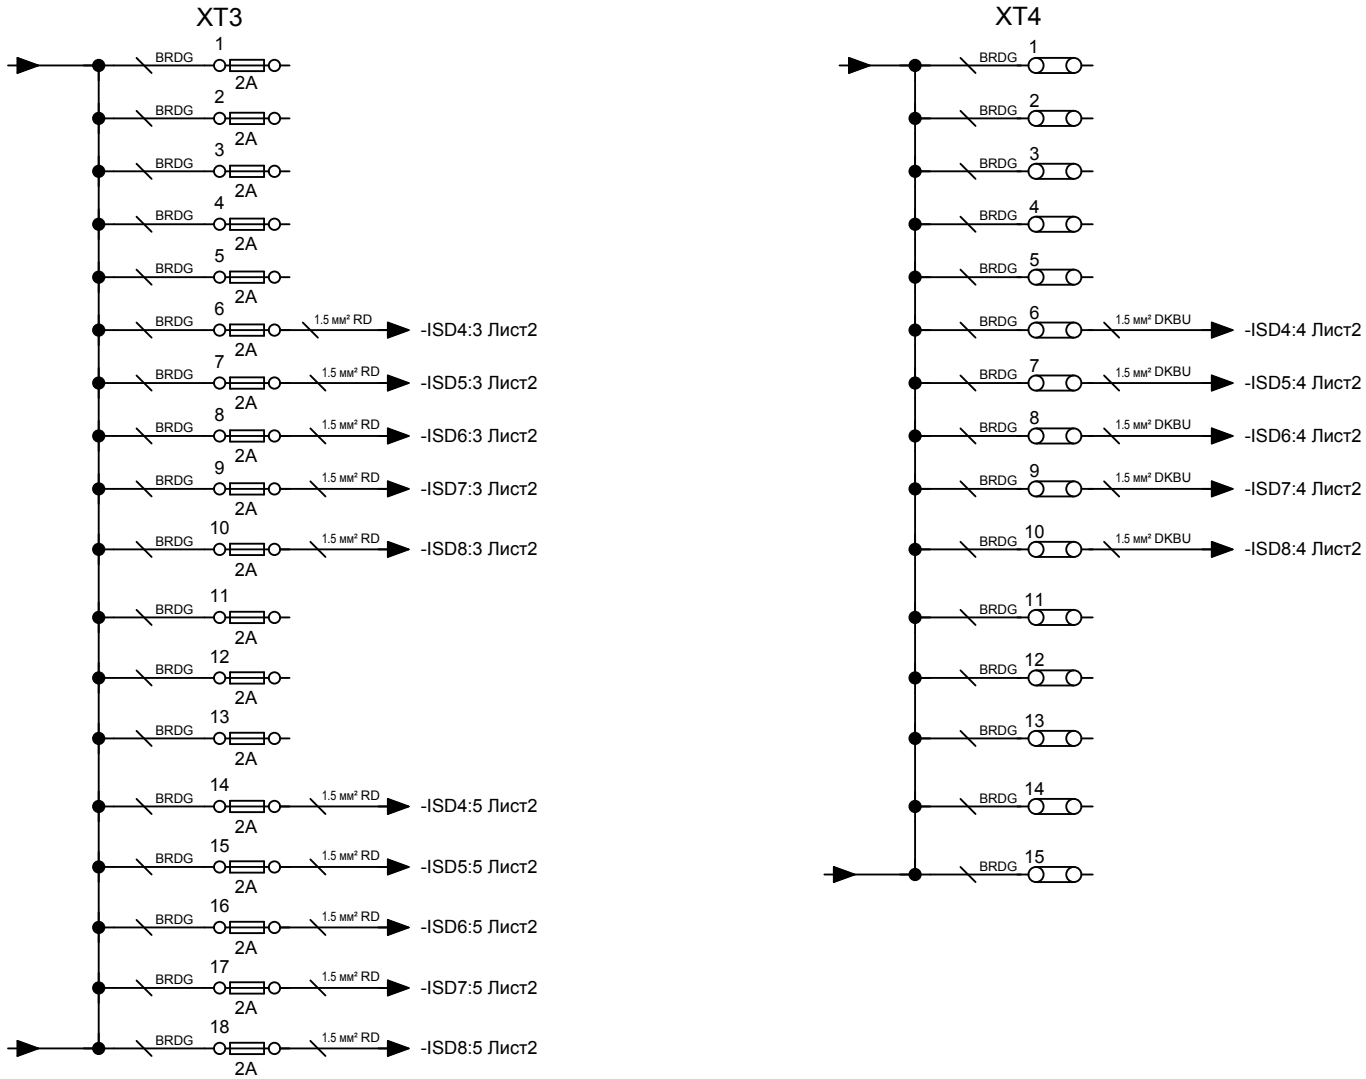

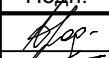Изм.	Лист	№ докум	Подп.	Дата
Разраб.	Аликин			01.2025
Пров.	Гиниятулин			01.2025
Н. контр.	Зырянова			01.2025
Утв.	Баянов			01.2025

Изм.	Лист	№ докум	Подп.	Дата
Разраб.	Аликин			
Пров.	Гиниятулин			
Н. контр.	Зырянова			
Утв.	Баянов			

Изм.	Лист	№ докум	Подп.	Дата
Разраб.	Аликин			
Пров.	Гиниятулин			
Н. контр.	Зырянова			
Утв.	Баянов			

Изм.	Лист	№ докум	Подп.	Дата
Разраб.	Аликин			
Пров.	Гиниятулин			
Н. контр.	Зырянова			
Утв.	Баянов			

Изм.	Лист	№ докум	Подп.	Дата
Разраб.	Аликин			
Пров.	Гиниятулин			
Н. контр.	Зырянова			
Утв.	Баянов			

Изм.	Лист	№ докум	Подп.	Дата
Разраб.	Аликин			
Пров.	Гиниятулин			
Н. контр.	Зырянова			
Утв.	Баянов			

Изм.	Лист	№ докум	Подп.	Дата
Разраб.	Аликин			
Пров.	Гиниятулин			
Н. контр.	Зырянова			
Утв.	Баянов			

Изм.	Лист	№ докум	Подп.	Дата
Разраб.	Аликин			
Разраб.	Аликин			
Пров.	Гиниятулин			
Н. контр.	Зырянова			

Инв. № подл.	Подп. и дата	Взам. инв. №	Инв. № дубл.	Подп. и дата


КOC25001-157-ACУ.08.Э4

Схема электропитания 24 VDC

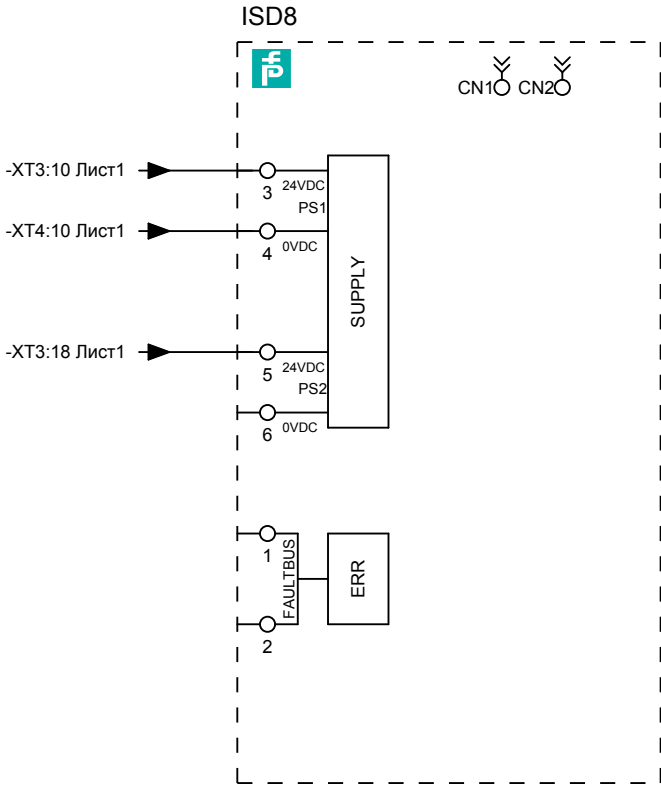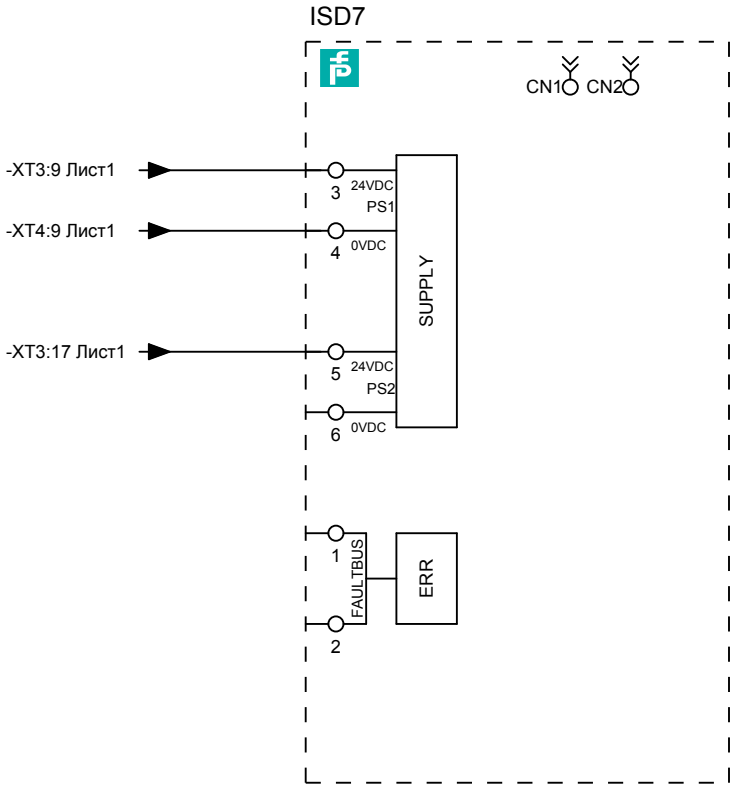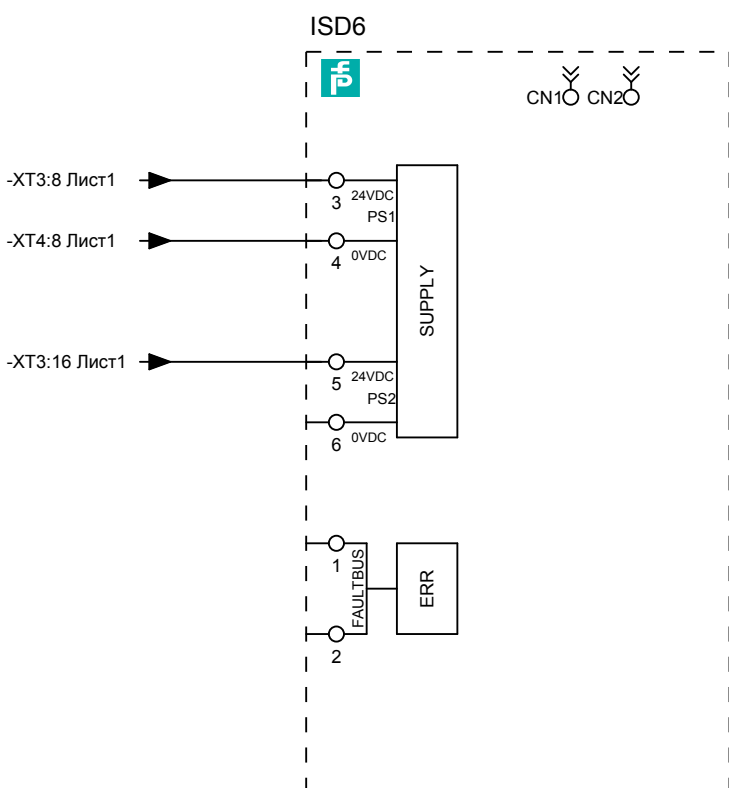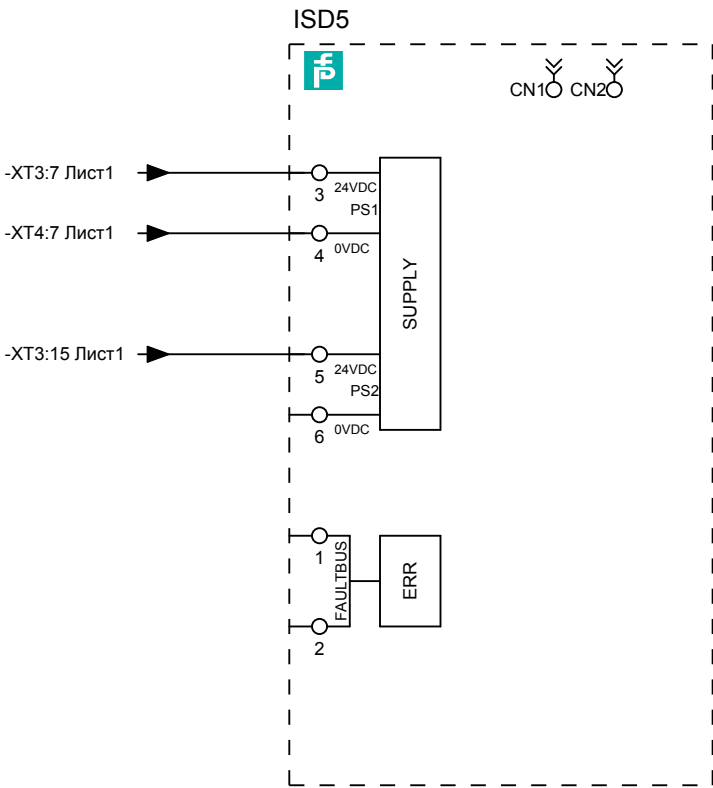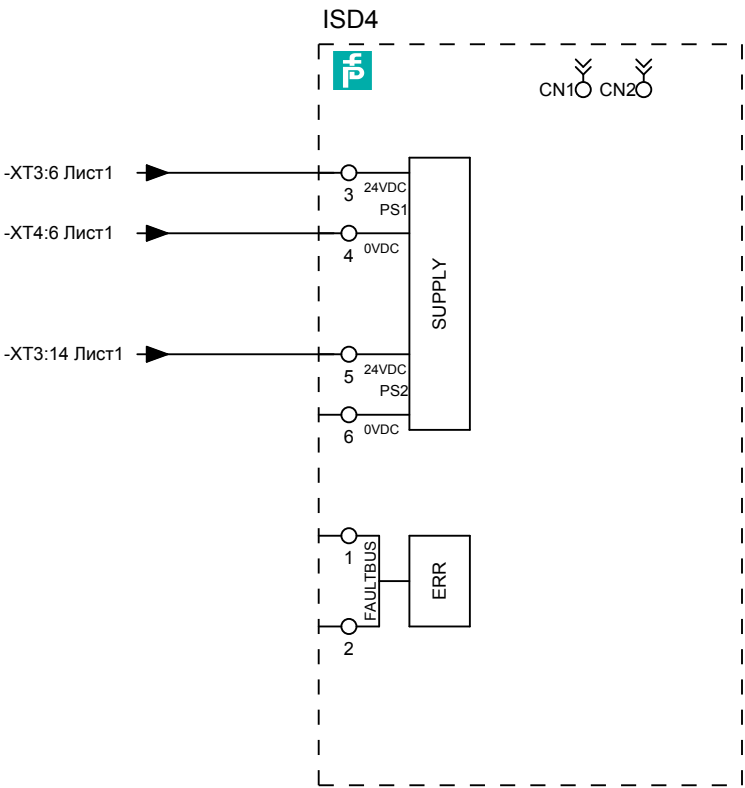

Изм	Лист	№ докум	Подп.	Дата

КOC25001-157-ACУ.08.Э4

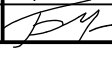Перв. примен.	Справ. №	Поз. обозначение	Описание				Кол.	Примечание									
		ХТ3	Предохранитель 5х20 мм,зак. № 2 А, 250 В				18	шт.									
		ISD4 ... ISD8	Терминальная плата,«Pepperl+Fuchs», зак. № HiCTB16-YC3-RRB-AK-CC-DX32				5	шт.									
Подп. и дата	Взам. инв. №	Инв. № дубл.	Подп. и дата														
Инв. № подл.	Изм	Лист	№ докум	Подп.	Дата	КОС25001-157-АСУ.08.ПЭ4											
						Шкаф №14 AI, АО, Namur. Перечень элементов											
												Разраб.	Аликин		01.2025	Лит.	Лист
Пров.	Гиниятулин		01.2025	Т		1	1										
Н. контр.	Зырянова		01.2025	 АСУ ИНЖИНИРИНГ													
Утв.	Баянов		01.2025														

Перв. примен.	Справ. №	Обозн. провода	Откуда идет		Куда поступает		Данные провода	Примечание
			Элемент	Конт.	Элемент	Конт.		
		ХТ3:17/ХТ3:18	ХТ3	17	ХТ3	18		BRDG
		ХТ3:16/ХТ3:18	ХТ3	16	ХТ3	18		BRDG
		ХТ3:15/ХТ3:18	ХТ3	15	ХТ3	18		BRDG
		ХТ3:14/ХТ3:18	ХТ3	14	ХТ3	18		BRDG
		ХТ3:13/ХТ3:18	ХТ3	13	ХТ3	18		BRDG
		ХТ3:12/ХТ3:18	ХТ3	12	ХТ3	18		BRDG
		ХТ3:11/ХТ3:18	ХТ3	11	ХТ3	18		BRDG
		ХТ3:10/ХТ3:18	ХТ3	10	ХТ3	18		BRDG
		ХТ3:9/ХТ3:18	ХТ3	9	ХТ3	18		BRDG
		ХТ3:8/ХТ3:18	ХТ3	8	ХТ3	18		BRDG
		ХТ3:7/ХТ3:18	ХТ3	7	ХТ3	18		BRDG
		ХТ3:6/ХТ3:18	ХТ3	6	ХТ3	18		BRDG
		ХТ3:5/ХТ3:18	ХТ3	5	ХТ3	18		BRDG
		ХТ3:4/ХТ3:18	ХТ3	4	ХТ3	18		BRDG
		ХТ3:3/ХТ3:18	ХТ3	3	ХТ3	18		BRDG
		ХТ3:2/ХТ3:18	ХТ3	2	ХТ3	18		BRDG
				ХТ3:1/ХТ3:18	ХТ3	1	ХТ3	18
ХТ4:14/ХТ4:15	ХТ4			14	ХТ4	15		BRDG
ХТ4:13/ХТ4:14	ХТ4			13	ХТ4	14		BRDG
ХТ4:12/ХТ4:13	ХТ4			12	ХТ4	13		BRDG
ХТ4:11/ХТ4:12	ХТ4			11	ХТ4	12		BRDG
ХТ4:10/ХТ4:11	ХТ4			10	ХТ4	11		BRDG
ХТ4:9/ХТ4:10	ХТ4			9	ХТ4	10		BRDG
ХТ4:8/ХТ4:9	ХТ4			8	ХТ4	9		BRDG
ХТ4:7/ХТ4:8	ХТ4			7	ХТ4	8		BRDG
ХТ4:6/ХТ4:7	ХТ4			6	ХТ4	7		BRDG
ХТ4:5/ХТ4:6	ХТ4			5	ХТ4	6		BRDG

Инв. № подл.	Подп. и дата	Взам. инв. №	Инв. № дубл.	Подп. и дата	Инв. № подл.

Обозн. провода	Откуда идет		Куда поступает		Данные провода	Примечание
	Элемент	Конт.	Элемент	Конт.		
XT4:4/XT4:5	XT4	4	XT4	5		BRDG
XT4:3/XT4:4	XT4	3	XT4	4		BRDG
XT4:2/XT4:3	XT4	2	XT4	3		BRDG
ISD7:5/XT3:17	ISD7	5	XT3	17	1.5 мм²	RD
ISD7:4/XT4:9	ISD7	4	XT4	9	1.5 мм²	DKBU
ISD7:3/XT3:9	ISD7	3	XT3	9	1.5 мм²	RD
ISD4:5/XT3:14	ISD4	5	XT3	14	1.5 мм²	RD
ISD4:4/XT4:6	ISD4	4	XT4	6	1.5 мм²	DKBU
ISD4:3/XT3:6	ISD4	3	XT3	6	1.5 мм²	RD
ISD8:5/XT3:18	ISD8	5	XT3	18	1.5 мм²	RD
ISD8:4/XT4:10	ISD8	4	XT4	10	1.5 мм²	DKBU
ISD8:3/XT3:10	ISD8	3	XT3	10	1.5 мм²	RD
ISD5:6/XT3:15	ISD5	5	XT3	15	1.5 мм²	RD
ISD5:4/XT4:7	ISD5	4	XT4	7	1.5 мм²	DKBU
ISD5:3/XT3:7	ISD5	3	XT3	7	1.5 мм²	RD
ISD6:6/XT3:16	ISD6	5	XT3	16	1.5 мм²	RD
ISD6:4/XT4:8	ISD6	4	XT4	8	1.5 мм²	DKBU
ISD6:3/XT3:8	ISD6	3	XT3	8	1.5 мм²	RD
			КОС25001-157-АСУ.08.ТБ			Лист
Изм	Лист	№ докум				Подп.