



Общество с ограниченной ответственностью

«АСУ Инжиниринг»

ПАО «Казаньоргсинтез»

МОДЕРНИЗАЦИЯ (МИГРАЦИЯ) АСУ ТП НИТКИ КОМПАУНДИРОВАНИЯ Д

ШБ159-1

Альбом 11

Всего альбомов 18

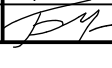
КОС25001-157-АСУ.11

 
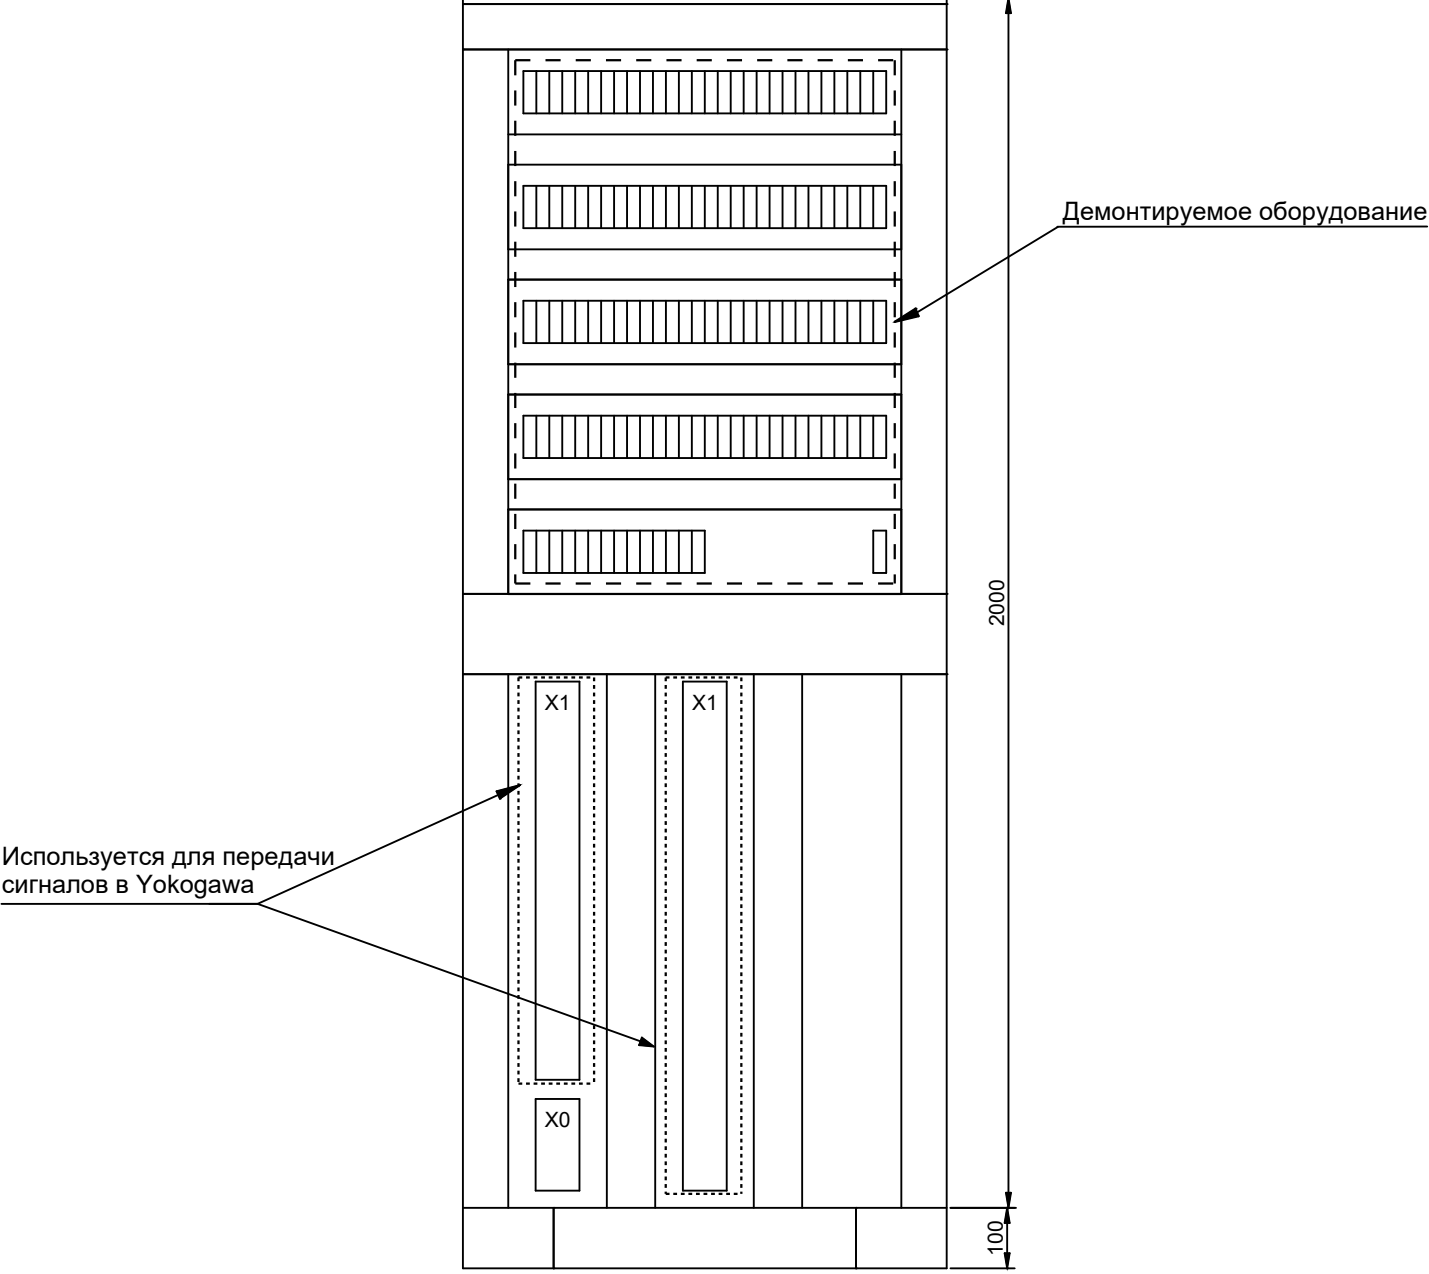
Главный инженер проекта

28.01.2025

Ф.Н. Баянов

Инв. № подл.	Подп. и дата	Взам. инв. №	Инв. № дубл.	Подп. и дата

Перв. примен.	Справ. №	№ строки	Формат	Обозначение	Наименование	Кол. листов	№ экз.	Примечание
		1		КОС25001-157-АСУ.11.ОП	ШБ159-1. Опись альбома	2		
		2		КОС25001-157-АСУ.11.ДМЧ	ШБ159-1. Демонтажный чертеж	1		
Подп. и дата	Взам. инв. №	Инв. № дубл.	Подп. и дата	КОС25001-157-АСУ.11.ОП				
Инв. № подл.	Изм	Лист	№ докум	Подп.	Дата	ШБ159-1. Опись альбома		
	Разраб.	Аликин		01.2025	Лит.	Лист	Листов	
	Пров.	Гиниятулин		01.2025				Т
	Н. контр.	Зырянова		01.2025	 АСУ ИНЖИНИРИНГ			
	Утв.	Баянов		01.2025				

Инв. № подл.	Подп. и дата	Взам. инв. №	Инв. № дубл.	Подп. и дата	Справ. №	Перв. примен.	ККС25001-157-АСУ.11.ДМЧ	
Вид спереди	
	
Вид спереди без дверей	
	
Примечание: Проводники от клеммников X1 к Siemens отключаются. К ним подключаются проектируемые магистральные кабели, идущие в Yokogawa. Подробное подключение представлено в документе ККС25001-157-АСУ.С6 "Таблица соединений и подключений".	
<table><tr><td></td><td></td><td></td><td></td><td></td></tr><tr><td></td><td></td><td></td><td></td><td></td></tr><tr><td></td><td></td><td></td><td></td><td></td></tr><tr><td>Изм.</td><td>Лист</td><td>№ докум</td><td>Подп.</td><td>Дата</td></tr><tr><td>Разраб.</td><td></td><td>Аликин</td><td></td><td>01.2025</td></tr><tr><td>Пров.</td><td></td><td>Гиниятулин</td><td></td><td>01.2025</td></tr><tr><td></td><td></td><td></td><td></td><td></td></tr><tr><td>Н. контр.</td><td></td><td>Зырянова</td><td></td><td>01.2025</td></tr><tr><td>Утв.</td><td></td><td>Баянов</td><td></td><td>01.2025</td></tr></table>																				Изм.	Лист	№ докум	Подп.	Дата	Разраб.		Аликин		01.2025	Пров.		Гиниятулин		01.2025						Н. контр.		Зырянова		01.2025	Утв.		Баянов		01.2025	<table><tr><td colspan="3">ККС25001-157-АСУ.11.ДМЧ</td></tr><tr><td colspan="3">ШБ159-1. Демонтажный чертеж</td></tr><tr><td>Лит.</td><td>Масса</td><td>Масштаб</td></tr><tr><td>Т</td><td></td><td>1:10</td></tr><tr><td colspan="2">Лист 1</td><td>Листов 1</td></tr><tr><td colspan="3"></td></tr></table>			ККС25001-157-АСУ.11.ДМЧ			ШБ159-1. Демонтажный чертеж			Лит.	Масса	Масштаб	Т		1:10	Лист 1		Листов 1			
Изм.	Лист	№ докум	Подп.	Дата	
Разраб.		Аликин		01.2025	
Пров.		Гиниятулин		01.2025	
Н. контр.		Зырянова		01.2025	
Утв.		Баянов		01.2025	
ККС25001-157-АСУ.11.ДМЧ	
ШБ159-1. Демонтажный чертеж	
Лит.	Масса	Масштаб	
Т		1:10	
Лист 1		Листов 1	
	
ККС25001-157-АСУ.11_Rev.0_01	